



*NOTE THAT ALL PLANIMETRIC DETAIL IS AS GROUND SURVEYED IN OCTOBER 2023 AND MUCH AS BEEN DESTROYED BY SUBSEQUENT STORMS. FIELD ADJUST IN COORDINATION WITH TOWN REPRESENTATIVES AT STRUCTURES IF STILL IN EXISTENCE.

NOTES

THE PURPOSE OF THIS PLAN IS TO SHOW THE EXISTING CONDITIONS AND PROPOSED BEACH NOURISHMENT ON SALISBURY BEACH AND IS PARTIALLY THE RESULT OF AN ON-THE-GROUND INSTRUMENT SURVEY PERFORMED BETWEEN SEPTEMBER 11 AND OCTOBER 20, 2023. EXISTING CONTOURS ARE BASED ON AUGUST 20, 2024 DOT LIDAR DATA IS POINT CLOUD DATA PARSED TO BARE EARTH AND PROVIDED TO THIS FIRM. DATUM IS NAVD88.

THERE ARE NO KNOWN UTILITIES IN THE AREA OF BEACH NOURISHMENT AS SHOWN. CONTRACTOR SHALL CONTACT "DIG-SAFE" FOR AN UNDERGROUND UTILITY MARKING AT 811 AT LEAST 72 HOURS PRIOR TO COMMENCEMENT OF ANY WORK OR AS OTHERWISE REQUIRED BY LAW.

BY GRAPHIC PLOTTING ONLY, THIS PROPERTY IS IN VARIOUS FLOOD ZONES AS SHOWN HEREON AS DEPICTED ON THE FLOOD INSURANCE RATE MAPS, COMMUNITY PANELS NO. 25009C0127F AND 25009C0129F WHICH BEAR AN EFFECTIVE DATE OF 07/02/2012 AND THE PROJECT AREA IS IN A SPECIAL FLOOD HAZARD AREA. NO FIELD SURVEYING WAS PERFORMED TO DETERMINE THIS ZONE.


NATURAL HERITAGE ESTIMATED HABITAT IS TAKEN FROM SHP FILES DOWNLOADED FROM MASS GIS. LIMIT OF ARTICLE 97 LANDS ARE THE LIMIT OF PRIVATE OWNERSHIP ALONG SALISBURY BEACH.

DESIGN AS DIRECTED AND COORDINATED BY HUGHES ENVIRONMENTAL CONSULTANTS. BEACH/DUNE INTERFACE IS AS PROVIDED BY HUGHES ENVIRONMENTAL CONSULTANTS BASED ON THE MARCH 2024 MASSDOT LIDAR.

OWNERSHIP INFORMATION USED IN THE PREPARATION OF THIS PLAN WAS OBTAINED FROM THE TOWN OF SALISBURY ASSESSOR'S OFFICES AND SOUTHERN ESSEX DISTRICT REGISTRY OF DEEDS INCLUDING THE LAND COURT. FOR OWNERSHIP OF THE BEACH SEE LAND COURT CERTIFICATE OF TITLE 10041.

ELEVATIONS ARE BASED ON NAVD88 AS ESTABLISHED BY RTK GPS.

TO THE BEST OF MY PROFESSIONAL KNOWLEDGE, INFORMATION, AND BELIEF, THIS PLAN CONFORMS TO THE TECHNICAL AND PROCEDURAL STANDARDS FOR THE PRACTICE OF LAND SURVEYING IN THE COMMONWEALTH OF MASSACHUSETTS.

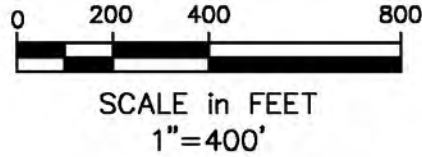

- MARCH 14, 2024 MASSDOT LIDAR MINOR CONTOUR
- MARCH 14, 2024 MASSDOT LIDAR MAJOR CONTOUR
- MARCH 14, 2024 MASSDOT LIDAR HIGHEST ASTRONOMICAL TIDE - EL. 5.95'
- MARCH 14, 2024 MASSDOT LIDAR MEAN HIGH WATER - EL. 3.82'
- MASS GIS ESTIMATED HABITAT
- MASS GIS FEMA FLOOD ZONE LIMITS
- DUNE BEACH INTERFACE
- PROPOSED BEACH NOURISHMENT CONTOUR
- PROPOSED BEACH NOURISHMENT CONTOUR - EL. 17
- PROPOSED BEACH NOURISHMENT LIMIT
- ARTICLE 97 LAND

Copyright 2024 Winter GEC, LLC

Winter GEC, LLC

44 MERRIMAC STREET
NEWBURYPORT, MA 01950
978-270-8626

SCALE:
HORIZ: 1"= 400'
VERT: N.A.

NO.	DATE	BY	REVISIONS	

FIELD: JK
CALCS: CO/EC
CHECKED: EJC
APPROVED: EJC

CONSERVATION PLAN
KEY SHEET


SALISBURY BEACH

PLAN OF LAND IN
SALISBURY, MASSACHUSETTS

SURVEYED FOR
HUGHES ENVIRONMENTAL

PROJECT NO.
2023-SAL-BEACH
DATE: AUG 18, 2024

SHEET NO.
KEY OF 15

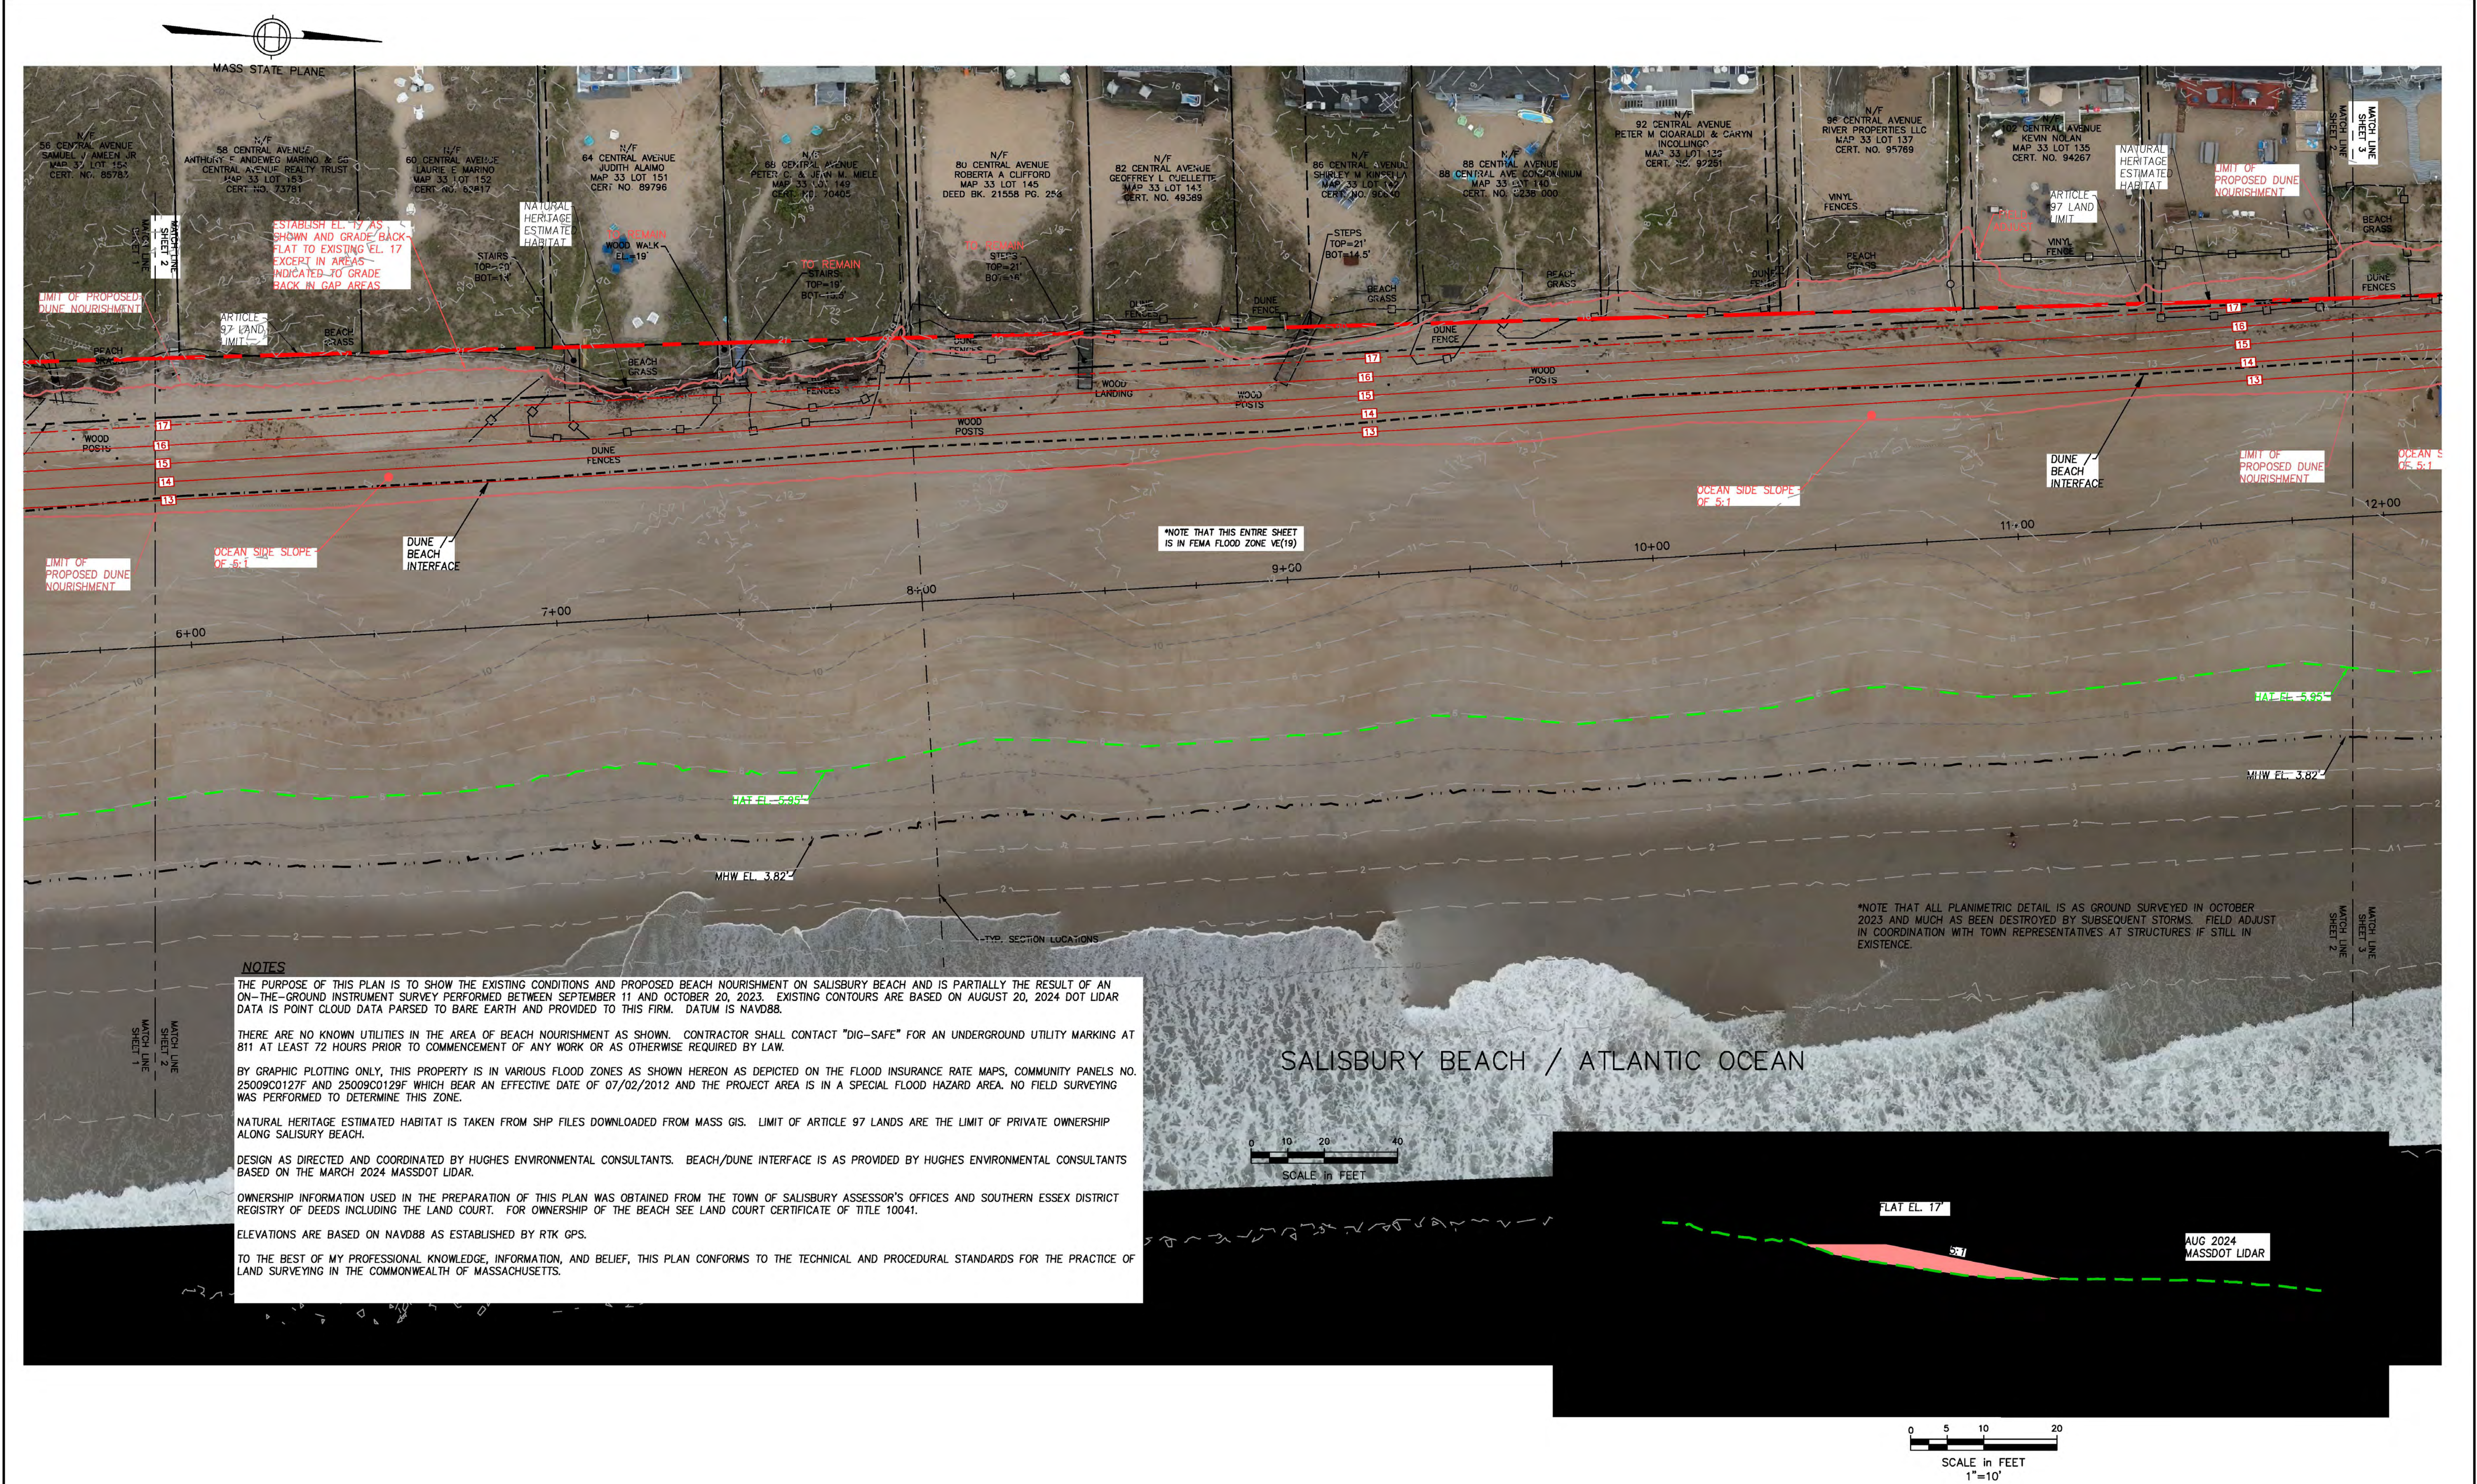

NOTES

THE PURPOSE OF THIS PLAN IS TO SHOW THE EXISTING CONDITIONS AND PROPOSED BEACH NOURISHMENT ON SALISBURY BEACH AND IS PARTIALLY THE RESULT OF AN ON-THE-GROUND INSTRUMENT SURVEY PERFORMED BETWEEN SEPTEMBER 11 AND OCTOBER 20, 2023. EXISTING CONTOURS ARE BASED ON AUGUST 20, 2024 DOT LIDAR DATA IS POINT CLOUD DATA PARSED TO BARE EARTH AND PROVIDED TO THIS FIRM. DATUM IS NAVD88.

THERE ARE NO KNOWN UTILITIES IN THE AREA OF BEACH NOURISHMENT AS SHOWN. CONTRACTOR SHALL CONTACT "DIG-SAFE" FOR AN UNDERGROUND UTILITY MARKING AT 811 AT LEAST 72 HOURS PRIOR TO COMMENCEMENT OF ANY WORK OR AS OTHERWISE REQUIRED BY LAW.

BY GRAPHIC PLOTTING ONLY, THIS PROPERTY IS IN VARIOUS FLOOD ZONES AS SHOWN HEREON AS DEPICTED ON THE FLOOD INSURANCE RATE MAPS, COMMUNITY PANELS NO. 25009C0127F AND 25009C0129F WHICH BEAR AN EFFECTIVE DATE OF 07/02/2012 AND THE PROJECT AREA IS IN A SPECIAL FLOOD HAZARD AREA. NO FIELD SURVEYING WAS PERFORMED TO DETERMINE THIS ZONE.


NATURAL HERITAGE ESTIMATED HABITAT IS TAKEN FROM SHP FILES DOWNLOADED FROM MASS GIS. LIMIT OF ARTICLE 97 LANDS ARE THE LIMIT OF PRIVATE OWNERSHIP ALONG SALISBURY BEACH.

DESIGN AS DIRECTED AND COORDINATED BY HUGHES ENVIRONMENTAL CONSULTANTS. BEACH/DUNE INTERFACE IS AS PROVIDED BY HUGHES ENVIRONMENTAL CONSULTANTS BASED ON THE MARCH 2024 MASSDOT LIDAR.

OWNERSHIP INFORMATION USED IN THE PREPARATION OF THIS PLAN WAS OBTAINED FROM THE TOWN OF SALISBURY ASSESSOR'S OFFICES AND SOUTHERN ESSEX DISTRICT REGISTRY OF DEEDS INCLUDING THE LAND COURT. FOR OWNERSHIP OF THE BEACH SEE LAND COURT CERTIFICATE OF TITLE 10041.

ELEVATIONS ARE BASED ON NAVD88 AS ESTABLISHED BY RTK GPS.

TO THE BEST OF MY PROFESSIONAL KNOWLEDGE, INFORMATION, AND BELIEF, THIS PLAN CONFORMS TO THE TECHNICAL AND PROCEDURAL STANDARDS FOR THE PRACTICE OF LAND SURVEYING IN THE COMMONWEALTH OF MASSACHUSETTS.

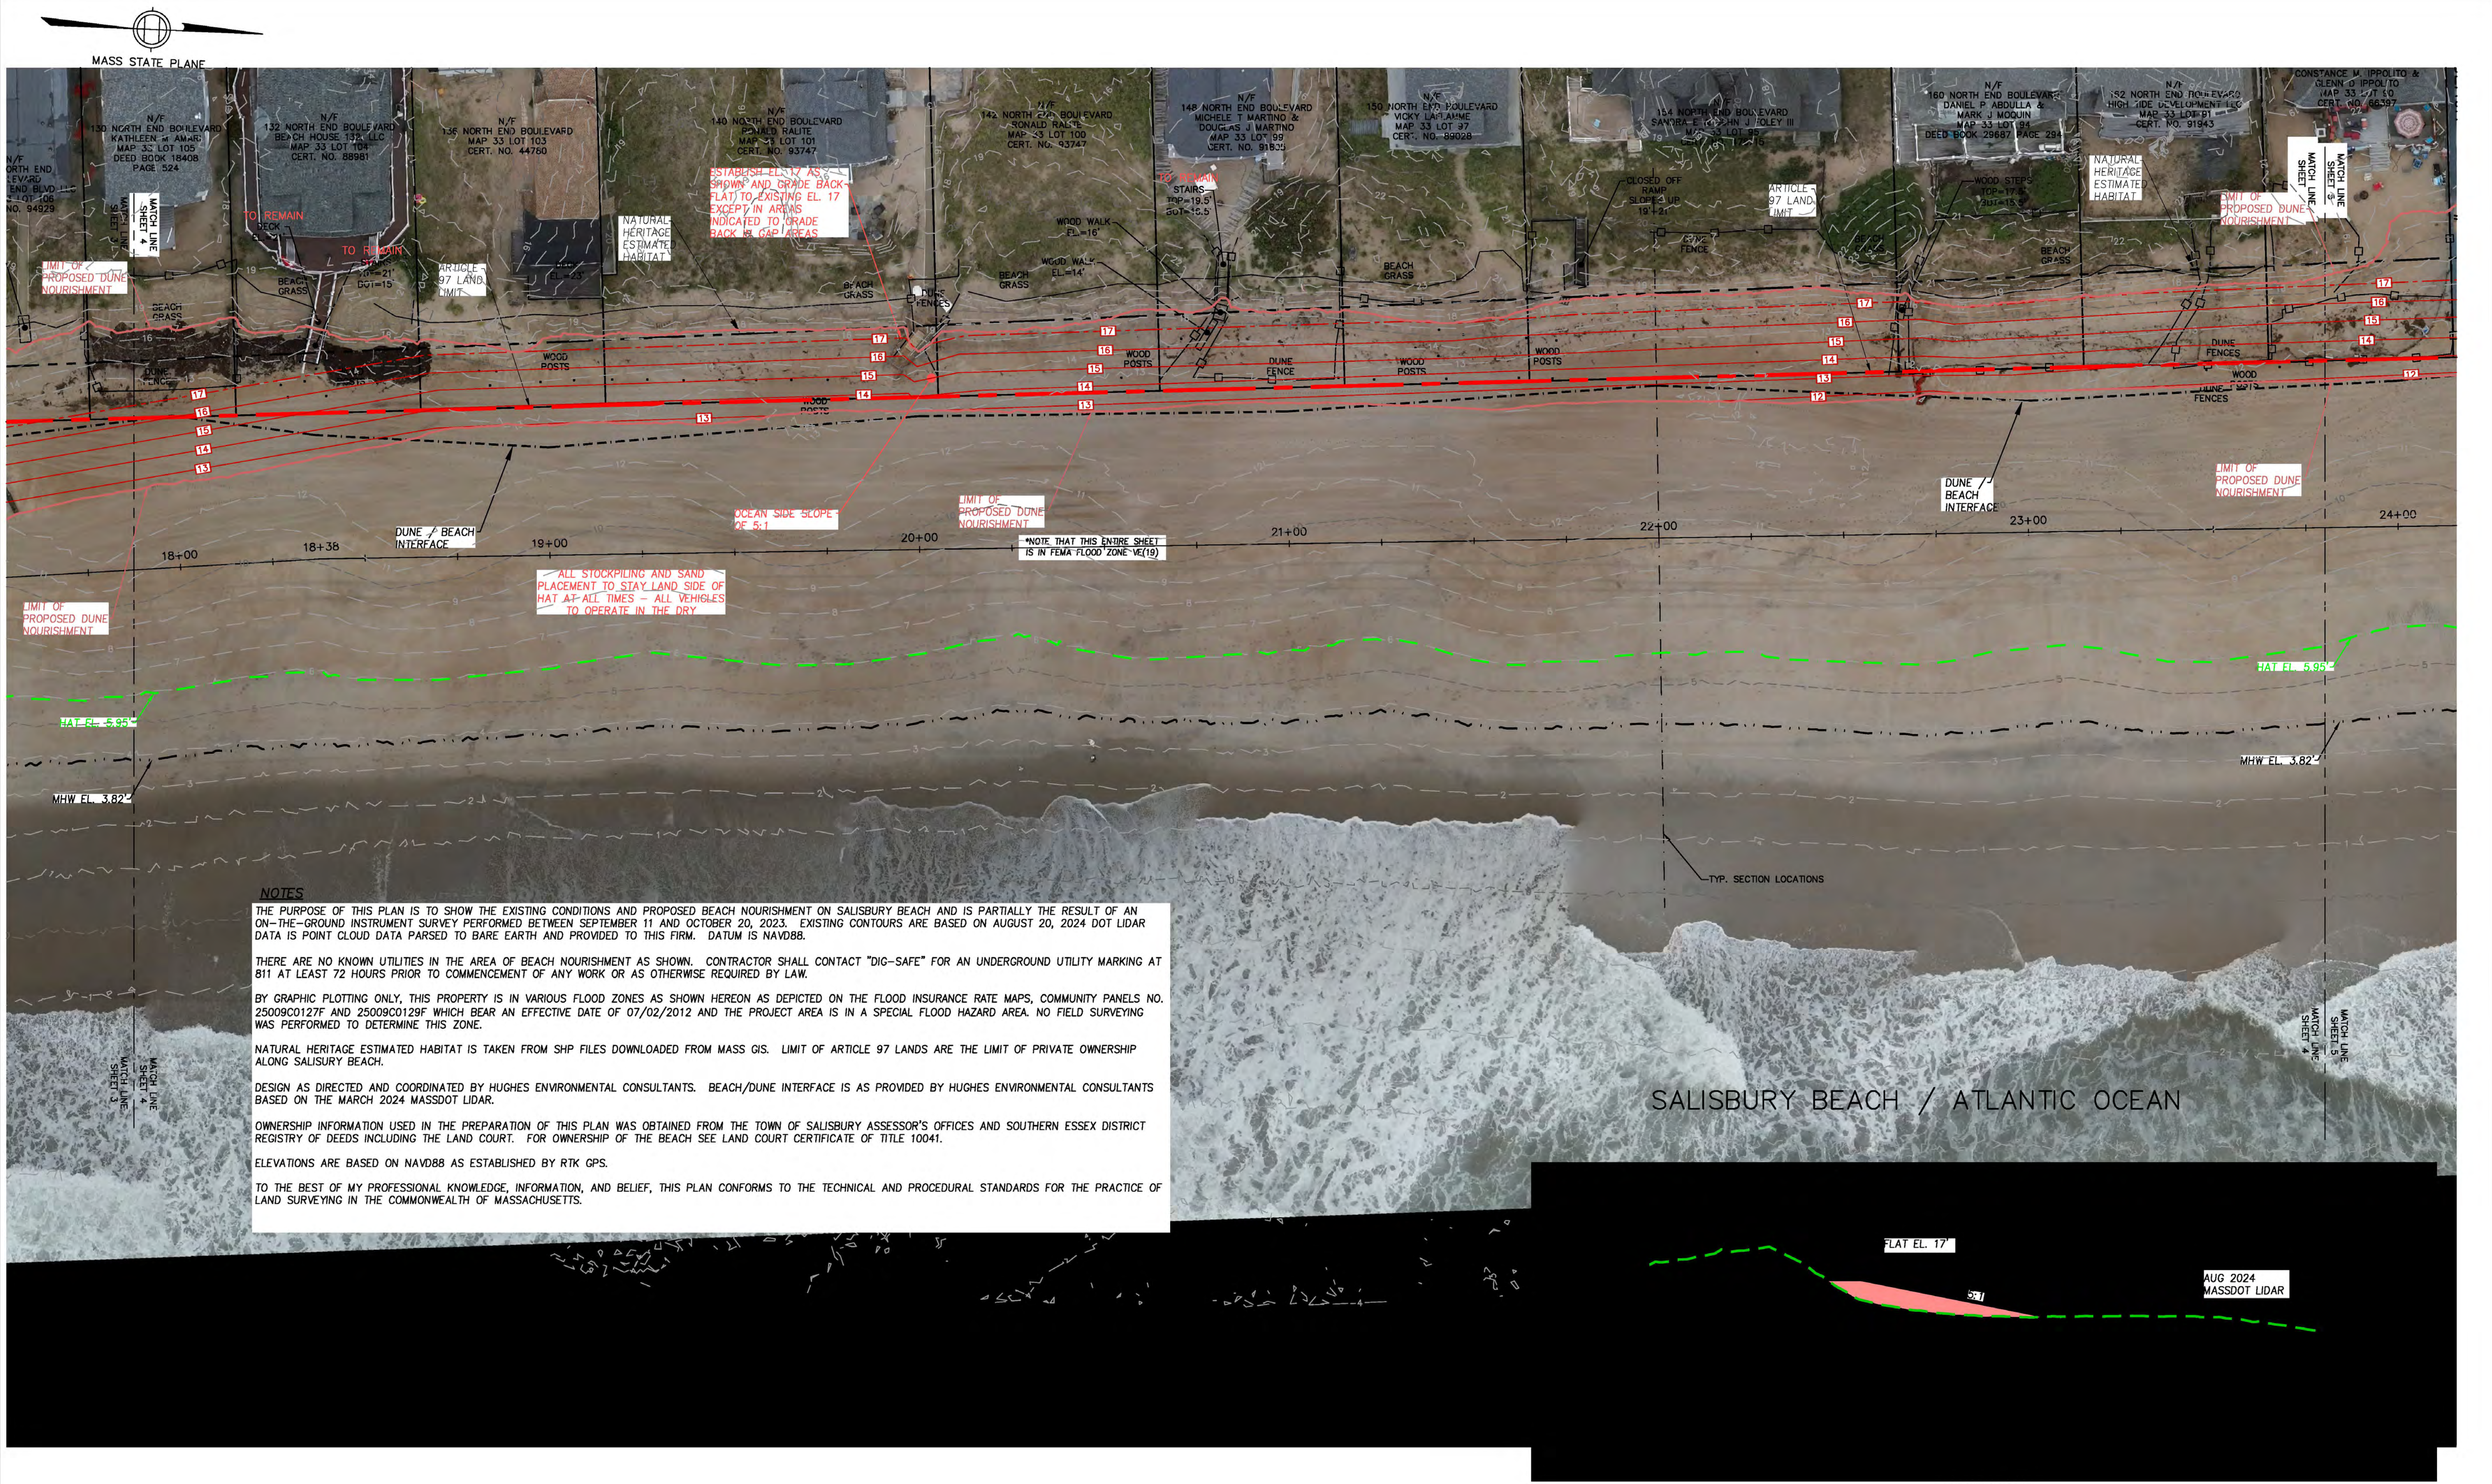

NOTES

THE PURPOSE OF THIS PLAN IS TO SHOW THE EXISTING CONDITIONS AND PROPOSED BEACH NOURISHMENT ON SALISBURY BEACH AND IS PARTIALLY THE RESULT OF AN ON-THE-GROUND INSTRUMENT SURVEY PERFORMED BETWEEN SEPTEMBER 11 AND OCTOBER 20, 2023. EXISTING CONTOURS ARE BASED ON AUGUST 20, 2024 DOT LIDAR DATA IS POINT CLOUD DATA PARSED TO BARE EARTH AND PROVIDED TO THIS FIRM. DATUM IS NAVD88.

THERE ARE NO KNOWN UTILITIES IN THE AREA OF BEACH NOURISHMENT AS SHOWN. CONTRACTOR SHALL CONTACT "DIG-SAFE" FOR AN UNDERGROUND UTILITY MARKING AT 811 AT LEAST 72 HOURS PRIOR TO COMMENCEMENT OF ANY WORK OR AS OTHERWISE REQUIRED BY LAW.

BY GRAPHIC PLOTTING ONLY, THIS PROPERTY IS IN VARIOUS FLOOD ZONES AS SHOWN HEREON AS DEPICTED ON THE FLOOD INSURANCE RATE MAPS, COMMUNITY PANELS NO. 25009C0127F AND 25009C0129F WHICH BEAR AN EFFECTIVE DATE OF 07/02/2012 AND THE PROJECT AREA IS IN A SPECIAL FLOOD HAZARD AREA. NO FIELD SURVEYING WAS PERFORMED TO DETERMINE THIS ZONE.

NATURAL HERITAGE ESTIMATED HABITAT IS TAKEN FROM SHP FILES DOWNLOADED FROM MASS GIS. LIMIT OF ARTICLE 97 LANDS ARE THE LIMIT OF PRIVATE OWNERSHIP ALONG SALISBURY BEACH.

DESIGN AS DIRECTED AND COORDINATED BY HUGHES ENVIRONMENTAL CONSULTANTS. BEACH/DUNE INTERFACE IS AS PROVIDED BY HUGHES ENVIRONMENTAL CONSULTANTS BASED ON THE MARCH 2024 MASSDOT LIDAR.

OWNERSHIP INFORMATION USED IN THE PREPARATION OF THIS PLAN WAS OBTAINED FROM THE TOWN OF SALISBURY ASSESSOR'S OFFICES AND SOUTHERN ESSEX DISTRICT REGISTRY OF DEEDS INCLUDING THE LAND COURT. FOR OWNERSHIP OF THE BEACH SEE LAND COURT CERTIFICATE OF TITLE 10041.

ELEVATIONS ARE BASED ON NAVD88 AS ESTABLISHED BY RTK GPS.

TO THE BEST OF MY PROFESSIONAL KNOWLEDGE, INFORMATION, AND BELIEF, THIS PLAN CONFORMS TO THE TECHNICAL AND PROCEDURAL STANDARDS FOR THE PRACTICE OF LAND SURVEYING IN THE COMMONWEALTH OF MASSACHUSETTS.

SCALE IN FEET
1"=10'

Copyright 2024 Winter GEC, LLC		Winter GEC, LLC		44 MERRIMAC STREET NEWBURYPORT, MA 01950 978-270-8626		SCALE: HORIZ: 1"= 20' VERT: N.A.		1 8/13/24 EJC REMOVE WORK FROM 150 CENTRAL AND 122 NORTH END BLVD		NO. DATE BY REVISIONS		FIELD: JK CALCS: CO/EC CHECKED: EJC APPROVED: EJC		CONSERVATION PLAN		SALISBURY BEACH		PLAN OF LAND IN SALISBURY, MASSACHUSETTS SURVEYED FOR HUGHES ENVIRONMENTAL		PROJECT NO. 2023-SAL-BEACH DATE: AUG 18, 2024		SHEET NO. 4 OF 15	
--------------------------------	--	-----------------	--	---	--	--	--	---	--	-----------------------	--	--	--	-------------------	--	-----------------	--	---	--	---	--	----------------------	--



NOTES

THE PURPOSE OF THIS PLAN IS TO SHOW THE EXISTING CONDITIONS AND PROPOSED BEACH NOURISHMENT ON SALISBURY BEACH AND IS PARTIALLY THE RESULT OF AN ON-THE-GROUND INSTRUMENT SURVEY PERFORMED BETWEEN SEPTEMBER 11 AND OCTOBER 20, 2023. EXISTING CONTOURS ARE BASED ON AUGUST 20, 2024 DOT LIDAR DATA IS POINT CLOUD DATA PARSED TO BARE EARTH AND PROVIDED TO THIS FIRM. DATUM IS NAVD88.

THERE ARE NO KNOWN UTILITIES IN THE AREA OF BEACH NOURISHMENT AS SHOWN. CONTRACTOR SHALL CONTACT "DIG-SAFE" FOR AN UNDERGROUND UTILITY MARKING AT 811 AT LEAST 72 HOURS PRIOR TO COMMENCEMENT OF ANY WORK OR AS OTHERWISE REQUIRED BY LAW.

BY GRAPHIC PLOTTING ONLY, THIS PROPERTY IS IN VARIOUS FLOOD ZONES AS SHOWN HEREON AS DEPICTED ON THE FLOOD INSURANCE RATE MAPS, COMMUNITY PANELS NO. 25009C0127F AND 25009C0129F WHICH BEAR AN EFFECTIVE DATE OF 07/02/2012 AND THE PROJECT AREA IS IN A SPECIAL FLOOD HAZARD AREA. NO FIELD SURVEYING WAS PERFORMED TO DETERMINE THIS ZONE.

NATURAL HERITAGE ESTIMATED HABITAT IS TAKEN FROM SHP FILES DOWNLOADED FROM MASS GIS. LIMIT OF ARTICLE 97 LANDS ARE THE LIMIT OF PRIVATE OWNERSHIP ALONG SALISBURY BEACH.

DESIGN AS DIRECTED AND COORDINATED BY HUGHES ENVIRONMENTAL CONSULTANTS. BEACH/DUNE INTERFACE IS AS PROVIDED BY HUGHES ENVIRONMENTAL CONSULTANTS BASED ON THE MARCH 2024 MASSDOT LIDAR.

OWNERSHIP INFORMATION USED IN THE PREPARATION OF THIS PLAN WAS OBTAINED FROM THE TOWN OF SALISBURY ASSESSOR'S OFFICES AND SOUTHERN ESSEX DISTRICT REGISTRY OF DEEDS INCLUDING THE LAND COURT. FOR OWNERSHIP OF THE BEACH SEE LAND COURT CERTIFICATE OF TITLE 10041.

ELEVATIONS ARE BASED ON NAVD88 AS ESTABLISHED BY RTK GPS.

TO THE BEST OF MY PROFESSIONAL KNOWLEDGE, INFORMATION, AND BELIEF, THIS PLAN CONFORMS TO THE TECHNICAL AND PROCEDURAL STANDARDS FOR THE PRACTICE OF LAND SURVEYING IN THE COMMONWEALTH OF MASSACHUSETTS.

SCALE in FEET
1"=10'

Copyright 2024 Winter GEC, LLC

Winter GEC, LLC

44 MERRIMAC STREET
NEWBURYPORT, MA 01950
978-270-8626

SCALE:
HORIZ: 1"= 20'
VERT: N.A.

NO.	DATE	BY	REVISIONS


FIELD: JK
CALCS: CO/EC
CHECKED: EJC
APPROVED: EJC

CONSERVATION PLAN

SALISBURY BEACH

PLAN OF LAND IN
SALISBURY, MASSACHUSETTS
SURVEYED FOR
HUGHES ENVIRONMENTAL

PROJECT NO.
2023-SAL-BEACH
DATE: AUG 18, 2024
SHEET NO.
5 OF 15

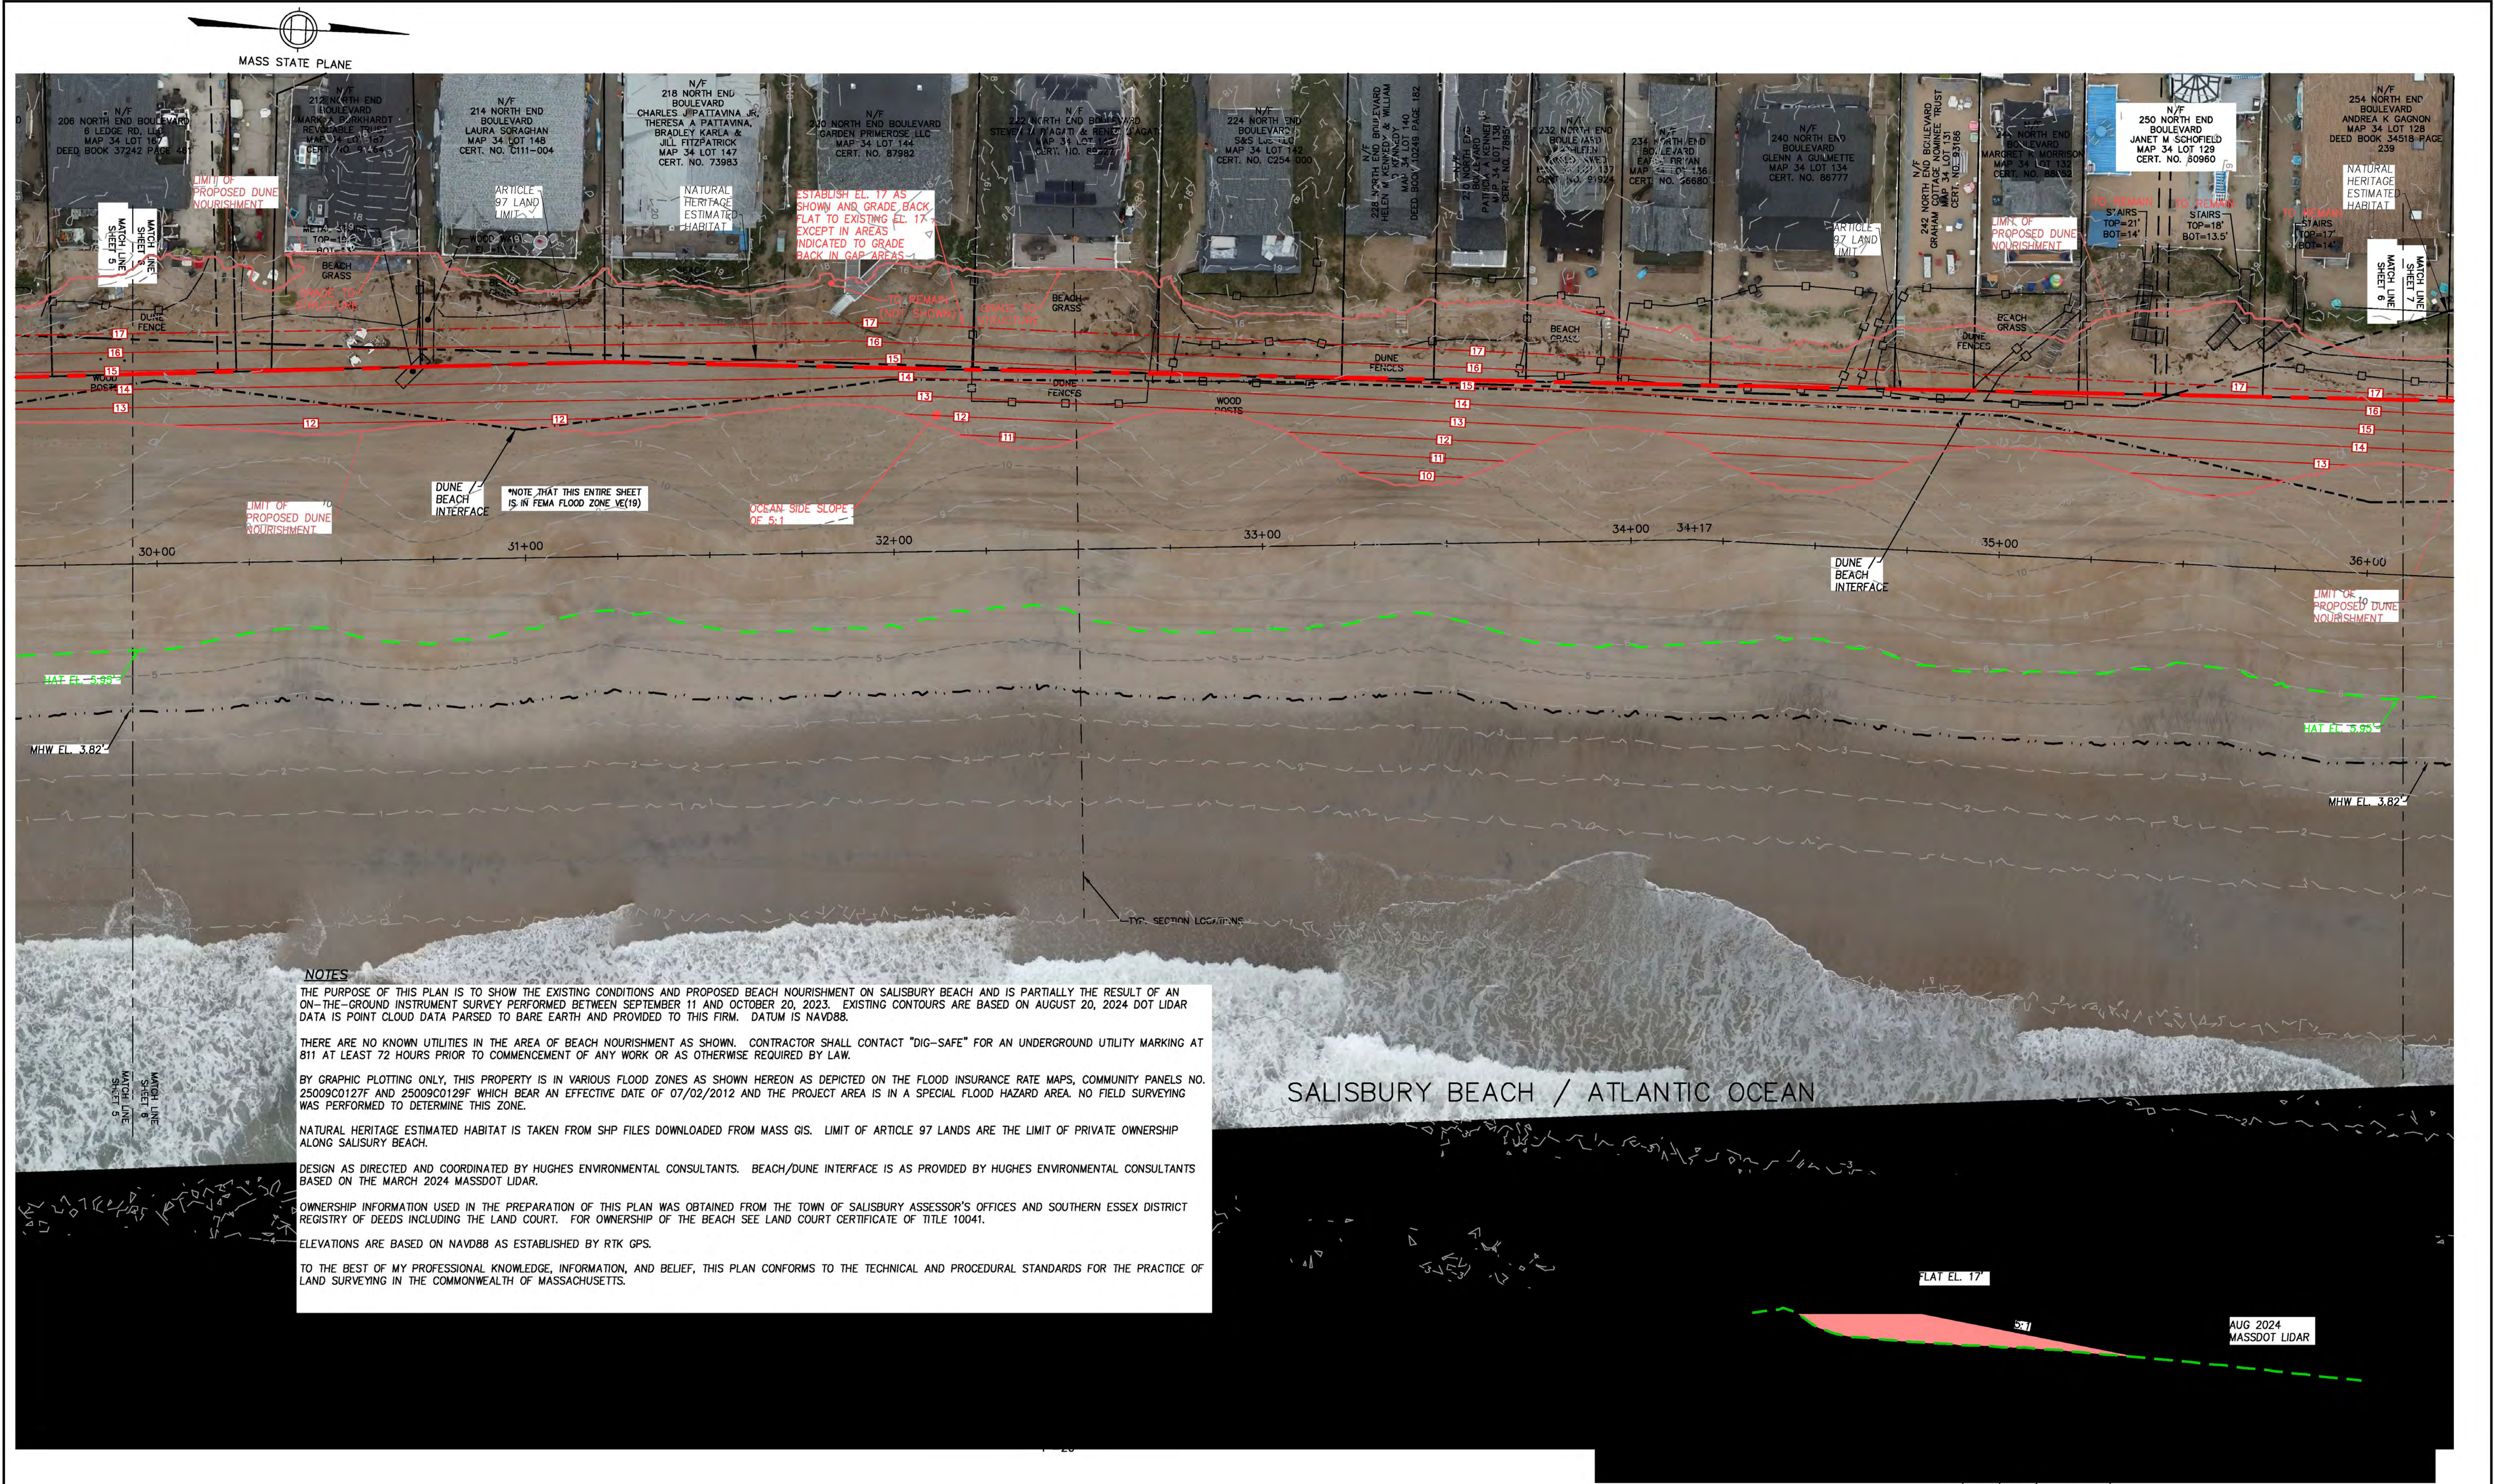

NOTES

THE PURPOSE OF THIS PLAN IS TO SHOW THE EXISTING CONDITIONS AND PROPOSED BEACH NOURISHMENT ON SALISBURY BEACH AND IS PARTIALLY THE RESULT OF AN ON-THE-GROUND INSTRUMENT SURVEY PERFORMED BETWEEN SEPTEMBER 11 AND OCTOBER 20, 2023. EXISTING CONTOURS ARE BASED ON AUGUST 20, 2024 DOT LIDAR DATA IS POINT CLOUD DATA PARSED TO BARE EARTH AND PROVIDED TO THIS FIRM. DATUM IS NAVD88.

THERE ARE NO KNOWN UTILITIES IN THE AREA OF BEACH NOURISHMENT AS SHOWN. CONTRACTOR SHALL CONTACT "DIG-SAFE" FOR AN UNDERGROUND UTILITY MARKING AT 811 AT LEAST 72 HOURS PRIOR TO COMMENCEMENT OF ANY WORK OR AS OTHERWISE REQUIRED BY LAW.

BY GRAPHIC PLOTTING ONLY, THIS PROPERTY IS IN VARIOUS FLOOD ZONES AS SHOWN HEREON AS DEPICTED ON THE FLOOD INSURANCE RATE MAPS, COMMUNITY PANELS NO. 25009C0127F AND 25009C0129F WHICH BEAR AN EFFECTIVE DATE OF 07/02/2012 AND THE PROJECT AREA IS IN A SPECIAL FLOOD HAZARD AREA. NO FIELD SURVEYING WAS PERFORMED TO DETERMINE THIS ZONE.

NATURAL HERITAGE ESTIMATED HABITAT IS TAKEN FROM SHP FILES DOWNLOADED FROM MASS GIS. LIMIT OF ARTICLE 97 LANDS ARE THE LIMIT OF PRIVATE OWNERSHIP ALONG SALISBURY BEACH.

DESIGN AS DIRECTED AND COORDINATED BY HUGHES ENVIRONMENTAL CONSULTANTS. BEACH/DUNE INTERFACE IS AS PROVIDED BY HUGHES ENVIRONMENTAL CONSULTANTS BASED ON THE MARCH 2024 MASSDOT LIDAR.

OWNERSHIP INFORMATION USED IN THE PREPARATION OF THIS PLAN WAS OBTAINED FROM THE TOWN OF SALISBURY ASSESSOR'S OFFICES AND SOUTHERN ESSEX DISTRICT REGISTRY OF DEEDS INCLUDING THE LAND COURT. FOR OWNERSHIP OF THE BEACH SEE LAND COURT CERTIFICATE OF TITLE 10041.

ELEVATIONS ARE BASED ON NAVD88 AS ESTABLISHED BY RTK GPS.

TO THE BEST OF MY PROFESSIONAL KNOWLEDGE, INFORMATION, AND BELIEF, THIS PLAN CONFORMS TO THE TECHNICAL AND PROCEDURAL STANDARDS FOR THE PRACTICE OF LAND SURVEYING IN THE COMMONWEALTH OF MASSACHUSETTS.

SCALE in FEET
1"=10'

Copyright 2024 Winter GEC, LLC

Winter GEC, LLC

44 MERRIMAC STREET
NEWBURYPORT, MA 01950
978-270-8626

SCALE:
HORIZ: 1"= 20'
VERT: N.A.

NO.	DATE	BY	REVISIONS	


FIELD: JK
CALCS: CO/EC
CHECKED: EJC
APPROVED: EJC

CONSERVATION PLAN

SALISBURY BEACH

PLAN OF LAND IN
SALISBURY, MASSACHUSETTS
SURVEYED FOR
HUGHES ENVIRONMENTAL

PROJECT NO.
2023-SAL-BEACH
DATE: AUG 18, 2024
SHEET NO.
6 OF 15

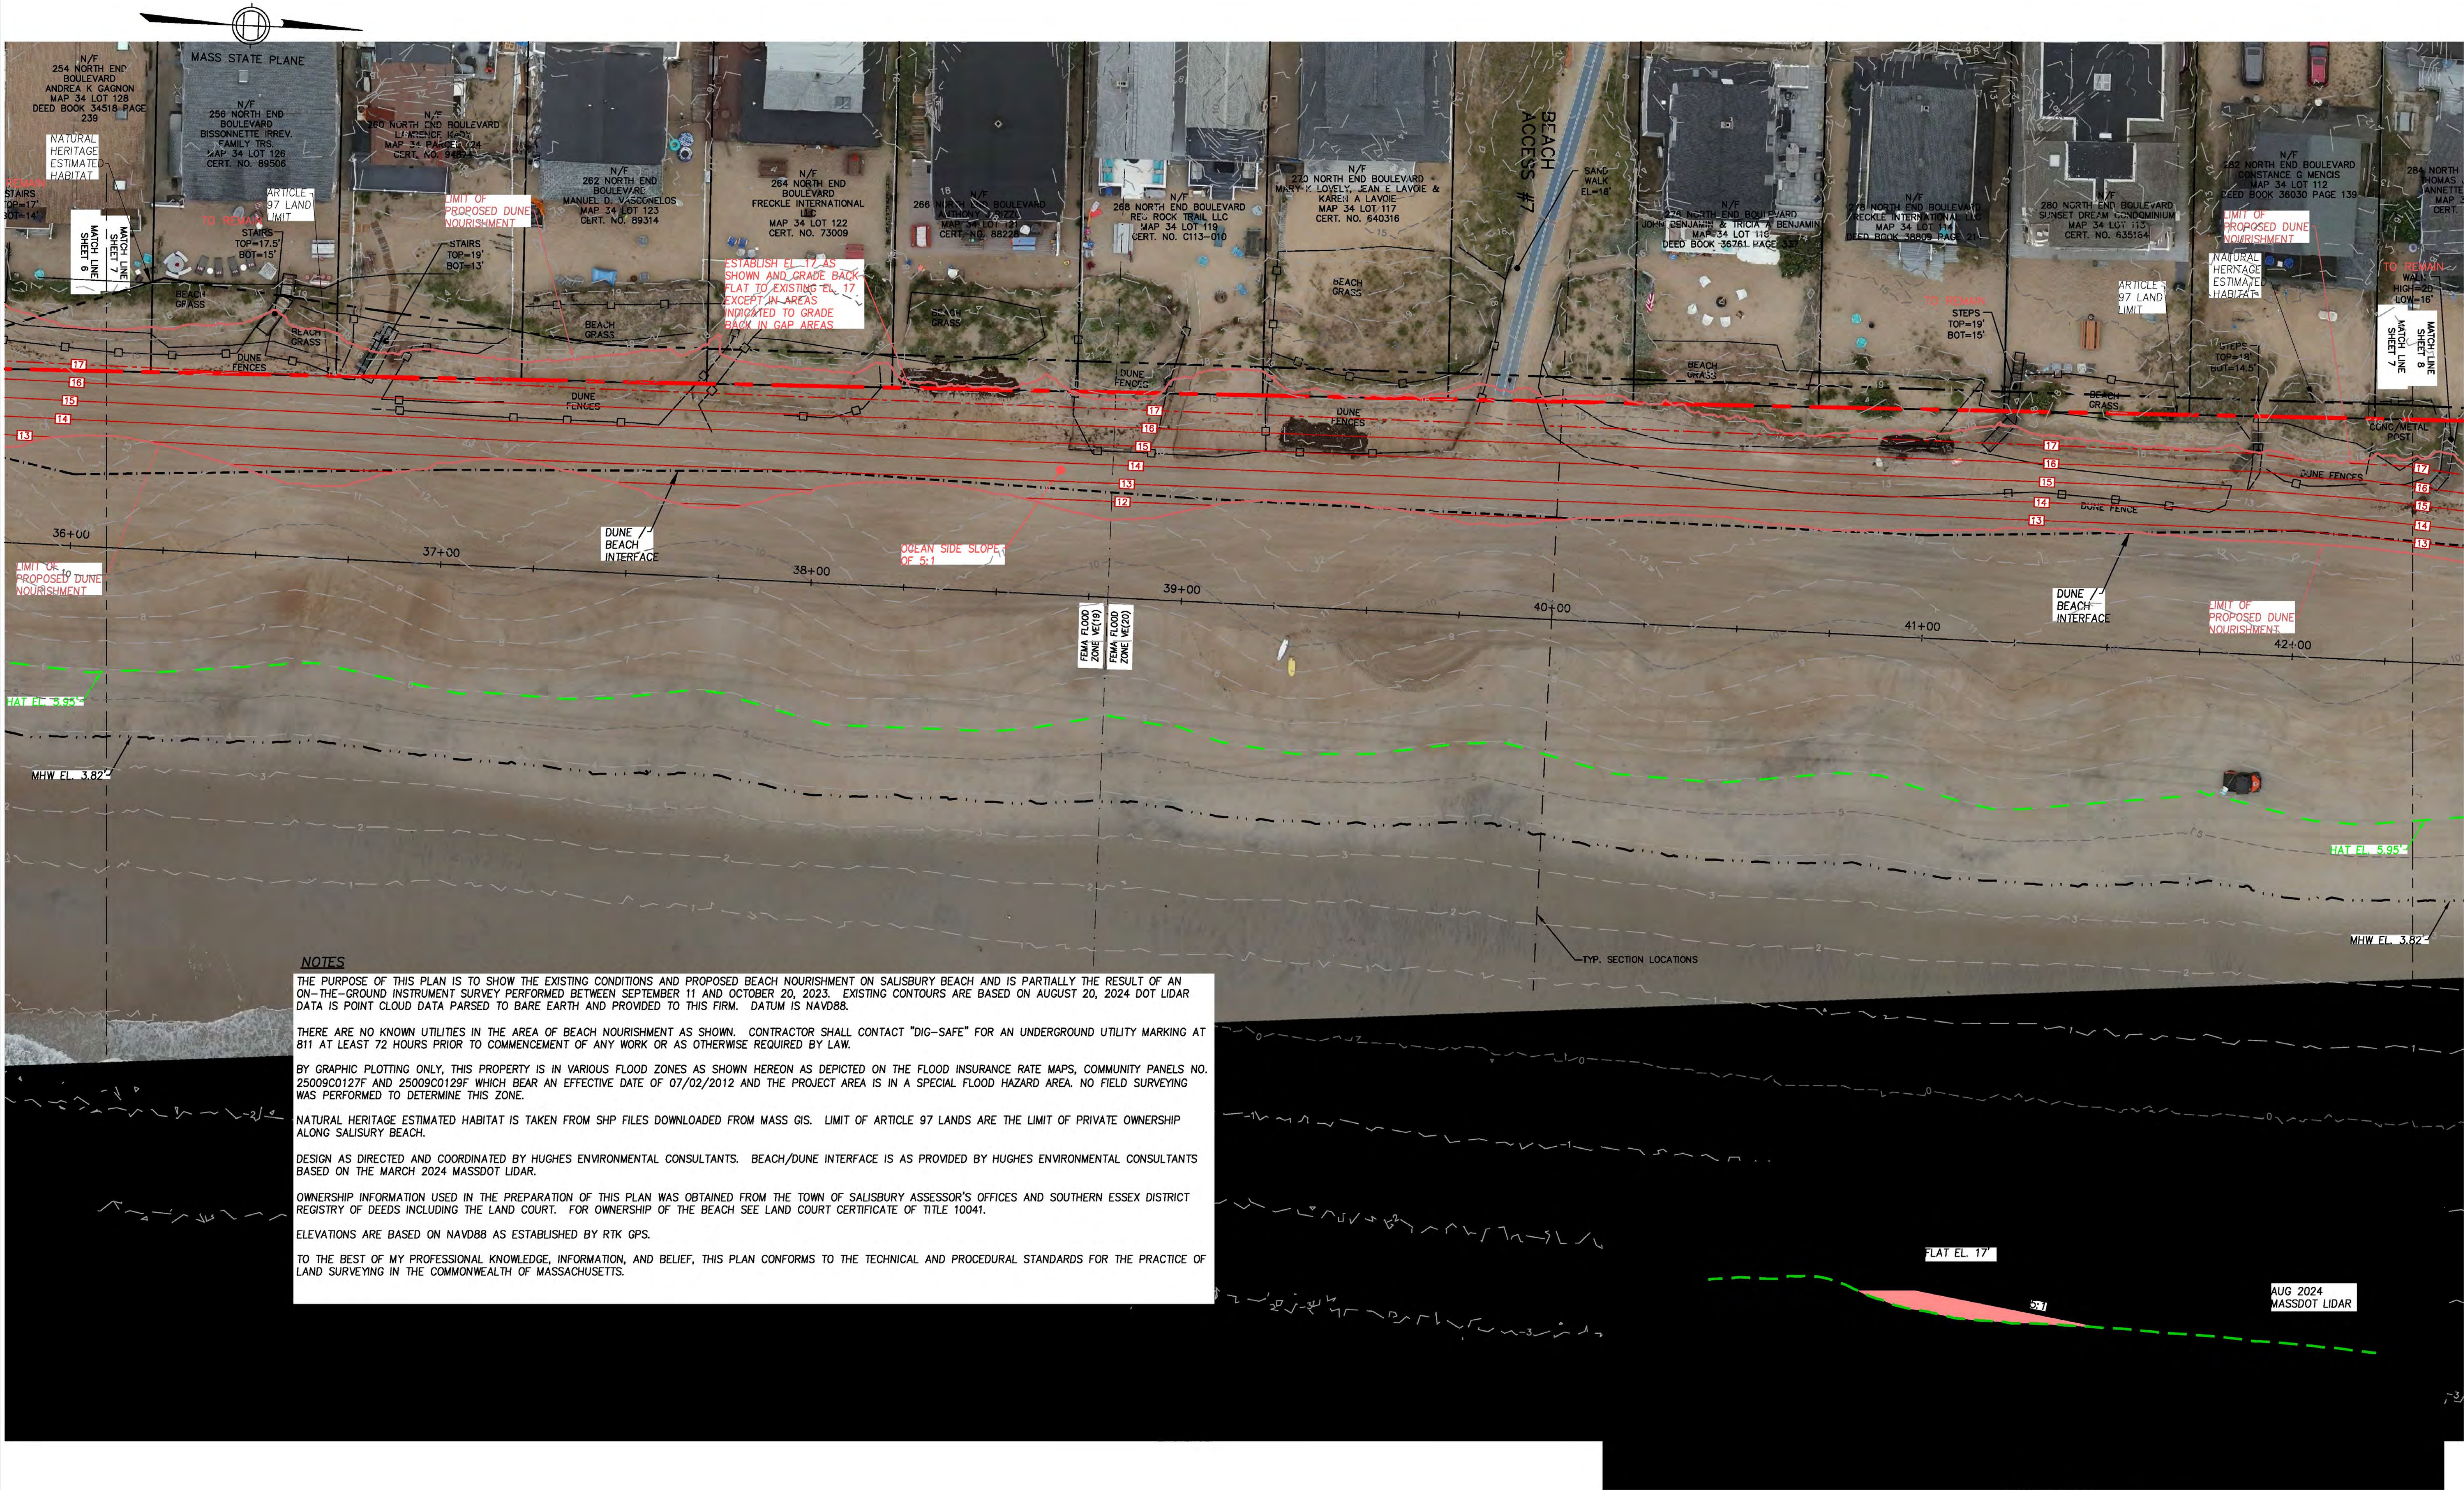

NOTES

THE PURPOSE OF THIS PLAN IS TO SHOW THE EXISTING CONDITIONS AND PROPOSED BEACH NOURISHMENT ON SALISBURY BEACH AND IS PARTIALLY THE RESULT OF AN ON-THE-GROUND INSTRUMENT SURVEY PERFORMED BETWEEN SEPTEMBER 11 AND OCTOBER 20, 2023. EXISTING CONTOURS ARE BASED ON AUGUST 20, 2024 DOT LIDAR DATA IS POINT CLOUD DATA PARSED TO BARE EARTH AND PROVIDED TO THIS FIRM. DATUM IS NAVD88.

THERE ARE NO KNOWN UTILITIES IN THE AREA OF BEACH NOURISHMENT AS SHOWN. CONTRACTOR SHALL CONTACT "DIG-SAFE" FOR AN UNDERGROUND UTILITY MARKING AT 811 AT LEAST 72 HOURS PRIOR TO COMMENCEMENT OF ANY WORK OR AS OTHERWISE REQUIRED BY LAW.

BY GRAPHIC PLOTTING ONLY, THIS PROPERTY IS IN VARIOUS FLOOD ZONES AS SHOWN HEREON AS DEPICTED ON THE FLOOD INSURANCE RATE MAPS, COMMUNITY PANELS NO. 25009C0127F AND 25009C0129F WHICH BEAR AN EFFECTIVE DATE OF 07/02/2012 AND THE PROJECT AREA IS IN A SPECIAL FLOOD HAZARD AREA. NO FIELD SURVEYING WAS PERFORMED TO DETERMINE THIS ZONE.

NATURAL HERITAGE ESTIMATED HABITAT IS TAKEN FROM SHP FILES DOWNLOADED FROM MASS GIS. LIMIT OF ARTICLE 97 LANDS ARE THE LIMIT OF PRIVATE OWNERSHIP ALONG SALISBURY BEACH.

DESIGN AS DIRECTED AND COORDINATED BY HUGHES ENVIRONMENTAL CONSULTANTS. BEACH/DUNE INTERFACE IS AS PROVIDED BY HUGHES ENVIRONMENTAL CONSULTANTS BASED ON THE MARCH 2024 MASSDOT LIDAR.

OWNERSHIP INFORMATION USED IN THE PREPARATION OF THIS PLAN WAS OBTAINED FROM THE TOWN OF SALISBURY ASSESSOR'S OFFICES AND SOUTHERN ESSEX DISTRICT REGISTRY OF DEEDS INCLUDING THE LAND COURT. FOR OWNERSHIP OF THE BEACH SEE LAND COURT CERTIFICATE OF TITLE 10041.

ELEVATIONS ARE BASED ON NAVD88 AS ESTABLISHED BY RTK GPS.

TO THE BEST OF MY PROFESSIONAL KNOWLEDGE, INFORMATION, AND BELIEF, THIS PLAN CONFORMS TO THE TECHNICAL AND PROCEDURAL STANDARDS FOR THE PRACTICE OF LAND SURVEYING IN THE COMMONWEALTH OF MASSACHUSETTS.

SCALE IN FEET
1"=10'

Copyright 2023 Winter GEC, LLC

Winter GEC, LLC

44 MERRIMAC STREET
NEWBURYPORT, MA 01950
978-270-8626

SCALE:
HORIZ: 1"= 20'
VERT: N.A.

NO.	DATE	BY	REVISIONS	

FIELD: JK
CALCS: CO/EC
CHECKED: EJC
APPROVED: EJC

CONSERVATION PLAN

SALISBURY BEACH

PLAN OF LAND IN
SALISBURY, MASSACHUSETTS
SURVEYED FOR
HUGHES ENVIRONMENTAL

PROJECT NO.
2023-SAL-BEACH
DATE: AUG 18, 2024
SHEET NO.
7 OF 15



NOTES

THE PURPOSE OF THIS PLAN IS TO SHOW THE EXISTING CONDITIONS AND PROPOSED BEACH NOURISHMENT ON SALISBURY BEACH AND IS PARTIALLY THE RESULT OF AN ON-THE-GROUND INSTRUMENT SURVEY PERFORMED BETWEEN SEPTEMBER 11 AND OCTOBER 20, 2023. EXISTING CONTOURS ARE BASED ON AUGUST 20, 2024 DOT LIDAR DATA IS POINT CLOUD DATA PARSED TO BARE EARTH AND PROVIDED TO THIS FIRM. DATUM IS NAVD88.

THERE ARE NO KNOWN UTILITIES IN THE AREA OF BEACH NOURISHMENT AS SHOWN. CONTRACTOR SHALL CONTACT "DIG-SAFE" FOR AN UNDERGROUND UTILITY MARKING AT B11 AT LEAST 72 HOURS PRIOR TO COMMENCEMENT OF ANY WORK OR AS OTHERWISE REQUIRED BY LAW.

BY GRAPHIC PLOTTING ONLY, THIS PROPERTY IS IN VARIOUS FLOOD ZONES AS SHOWN HEREON AS DEPICTED ON THE FLOOD INSURANCE RATE MAPS, COMMUNITY PANELS NO. 25009C0127F AND 25009C0129F WHICH BEAR AN EFFECTIVE DATE OF 07/02/2012 AND THE PROJECT AREA IS IN A SPECIAL FLOOD HAZARD AREA. NO FIELD SURVEYING WAS PERFORMED TO DETERMINE THIS ZONE.


NATURAL HERITAGE ESTIMATED HABITAT IS TAKEN FROM SHP FILES DOWNLOADED FROM MASS GIS. LIMIT OF ARTICLE 97 LANDS ARE THE LIMIT OF PRIVATE OWNERSHIP ALONG SALISBURY BEACH.

DESIGN AS DIRECTED AND COORDINATED BY HUGHES ENVIRONMENTAL CONSULTANTS. BEACH/DUNE INTERFACE IS AS PROVIDED BY HUGHES ENVIRONMENTAL CONSULTANTS BASED ON THE MARCH 2024 MASSDOT LIDAR.


OWNERSHIP INFORMATION USED IN THE PREPARATION OF THIS PLAN WAS OBTAINED FROM THE TOWN OF SALISBURY ASSESSOR'S OFFICES AND SOUTHERN ESSEX DISTRICT REGISTRY OF DEEDS INCLUDING THE LAND COURT. FOR OWNERSHIP OF THE BEACH SEE LAND COURT CERTIFICATE OF TITLE 10041.

ELEVATIONS ARE BASED ON NAVD88 AS ESTABLISHED BY RTK GPS.

TO THE BEST OF MY PROFESSIONAL KNOWLEDGE, INFORMATION, AND BELIEF, THIS PLAN CONFORMS TO THE TECHNICAL AND PROCEDURAL STANDARDS FOR THE PRACTICE OF LAND SURVEYING IN THE COMMONWEALTH OF MASSACHUSETTS.

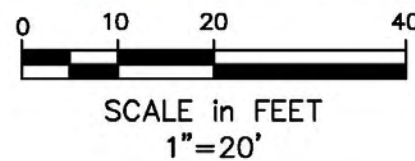

*NOTE THAT ALL PLANIMETRIC DETAIL IS AS GROUND SURVEYED IN OCTOBER 2023 AND MUCH AS BEEN DESTROYED BY SUBSEQUENT STORMS. FIELD ADJUST IN COORDINATION WITH TOWN REPRESENTATIVES AT STRUCTURES IF STILL IN EXISTENCE.

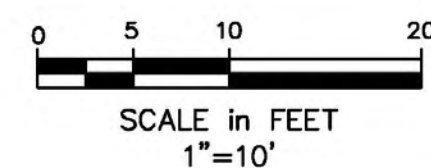

Copyright 2023 Winter GEC, LLC

Winter GEC, LLC

44 MERRIMAC STREET
NEWBURYPORT, MA 01950
978-270-8626

SCALE:
HORIZ: 1"= 20'
VERT: N.A.

NO.	DATE	BY	REVISIONS
1	8/13/24	EJC	CORRECT SECTION STATION LABELING

FIELD: JK
CALCS: CO/EC
CHECKED: EJC
APPROVED: EJC

CONSERVATION PLAN

SALISBURY BEACH

PLAN OF LAND IN
SALISBURY, MASSACHUSETTS
SURVEYED FOR
HUGHES ENVIRONMENTAL

PROJECT NO.
2023-SAL-BEACH
DATE: AUG 18, 2024
SHEET NO.
9 OF 15



NOTES

THE PURPOSE OF THIS PLAN IS TO SHOW THE EXISTING CONDITIONS AND PROPOSED BEACH NOURISHMENT ON SALISBURY BEACH AND IS PARTIALLY THE RESULT OF AN ON-THE-GROUND INSTRUMENT SURVEY PERFORMED BETWEEN SEPTEMBER 11 AND OCTOBER 20, 2023. EXISTING CONTOURS ARE BASED ON AUGUST 20, 2024 DOT LIDAR DATA IS POINT CLOUD DATA PARSED TO BARE EARTH AND PROVIDED TO THIS FIRM. DATUM IS NAVD88.

THERE ARE NO KNOWN UTILITIES IN THE AREA OF BEACH NOURISHMENT AS SHOWN. CONTRACTOR SHALL CONTACT "DIG-SAFE" FOR AN UNDERGROUND UTILITY MARKING AT 811 AT LEAST 72 HOURS PRIOR TO COMMENCEMENT OF ANY WORK OR AS OTHERWISE REQUIRED BY LAW.

BY GRAPHIC PLOTTING ONLY, THIS PROPERTY IS IN VARIOUS FLOOD ZONES AS SHOWN HEREON AS DEPICTED ON THE FLOOD INSURANCE RATE MAPS, COMMUNITY PANELS NO. 25009C0127F AND 25009C0129F WHICH BEAR AN EFFECTIVE DATE OF 07/02/2012 AND THE PROJECT AREA IS IN A SPECIAL FLOOD HAZARD AREA. NO FIELD SURVEYING WAS PERFORMED TO DETERMINE THIS ZONE.


NATURAL HERITAGE ESTIMATED HABITAT IS TAKEN FROM SHP FILES DOWNLOADED FROM MASS GIS. LIMIT OF ARTICLE 97 LANDS ARE THE LIMIT OF PRIVATE OWNERSHIP ALONG SALISBURY BEACH.

DESIGN AS DIRECTED AND COORDINATED BY HUGHES ENVIRONMENTAL CONSULTANTS. BEACH/DUNE INTERFACE IS AS PROVIDED BY HUGHES ENVIRONMENTAL CONSULTANTS BASED ON THE MARCH 2024 MASSDOT LIDAR.

OWNERSHIP INFORMATION USED IN THE PREPARATION OF THIS PLAN WAS OBTAINED FROM THE TOWN OF SALISBURY ASSESSOR'S OFFICES AND SOUTHERN ESSEX DISTRICT REGISTRY OF DEEDS INCLUDING THE LAND COURT. FOR OWNERSHIP OF THE BEACH SEE LAND COURT CERTIFICATE OF TITLE 10041.

ELEVATIONS ARE BASED ON NAVD88 AS ESTABLISHED BY RTK GPS.

TO THE BEST OF MY PROFESSIONAL KNOWLEDGE, INFORMATION, AND BELIEF, THIS PLAN CONFORMS TO THE TECHNICAL AND PROCEDURAL STANDARDS FOR THE PRACTICE OF LAND SURVEYING IN THE COMMONWEALTH OF MASSACHUSETTS.

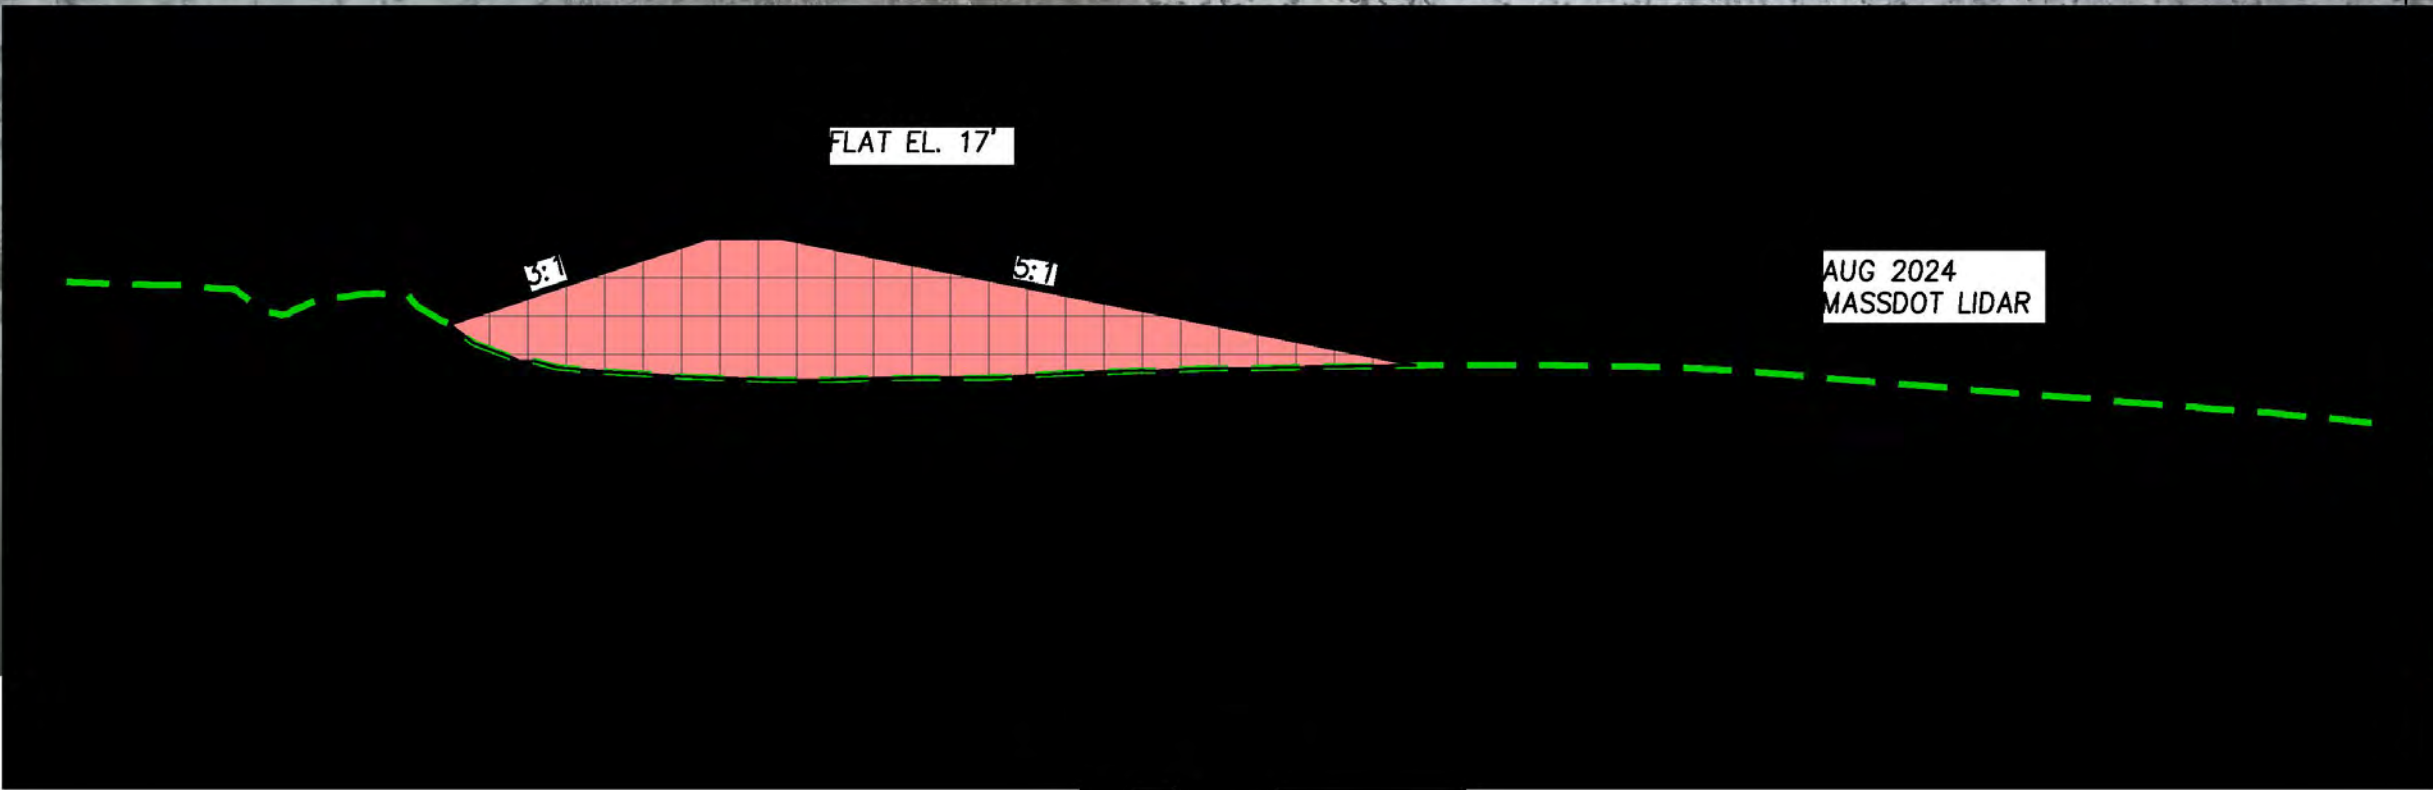

Copyright 2023 Winter GEC, LLC

Winter GEC, LLC

44 MERRIMAC STREET
NEWBURYPORT, MA 01950
978-270-8626

SCALE:
HORIZ: 1"= 20'
VERT: N.A.

NO.	DATE	BY	REVISIONS


FIELD: JK
CALCS: CO/EC
CHECKED: EJC
APPROVED: EJC

CONSERVATION PLAN

SALISBURY BEACH

PLAN OF LAND IN
SALISBURY, MASSACHUSETTS
SURVEYED FOR
HUGHES ENVIRONMENTAL

PROJECT NO.
2023-SAL-BEACH
DATE: AUG 18, 2024
SHEET NO.
12 OF 15

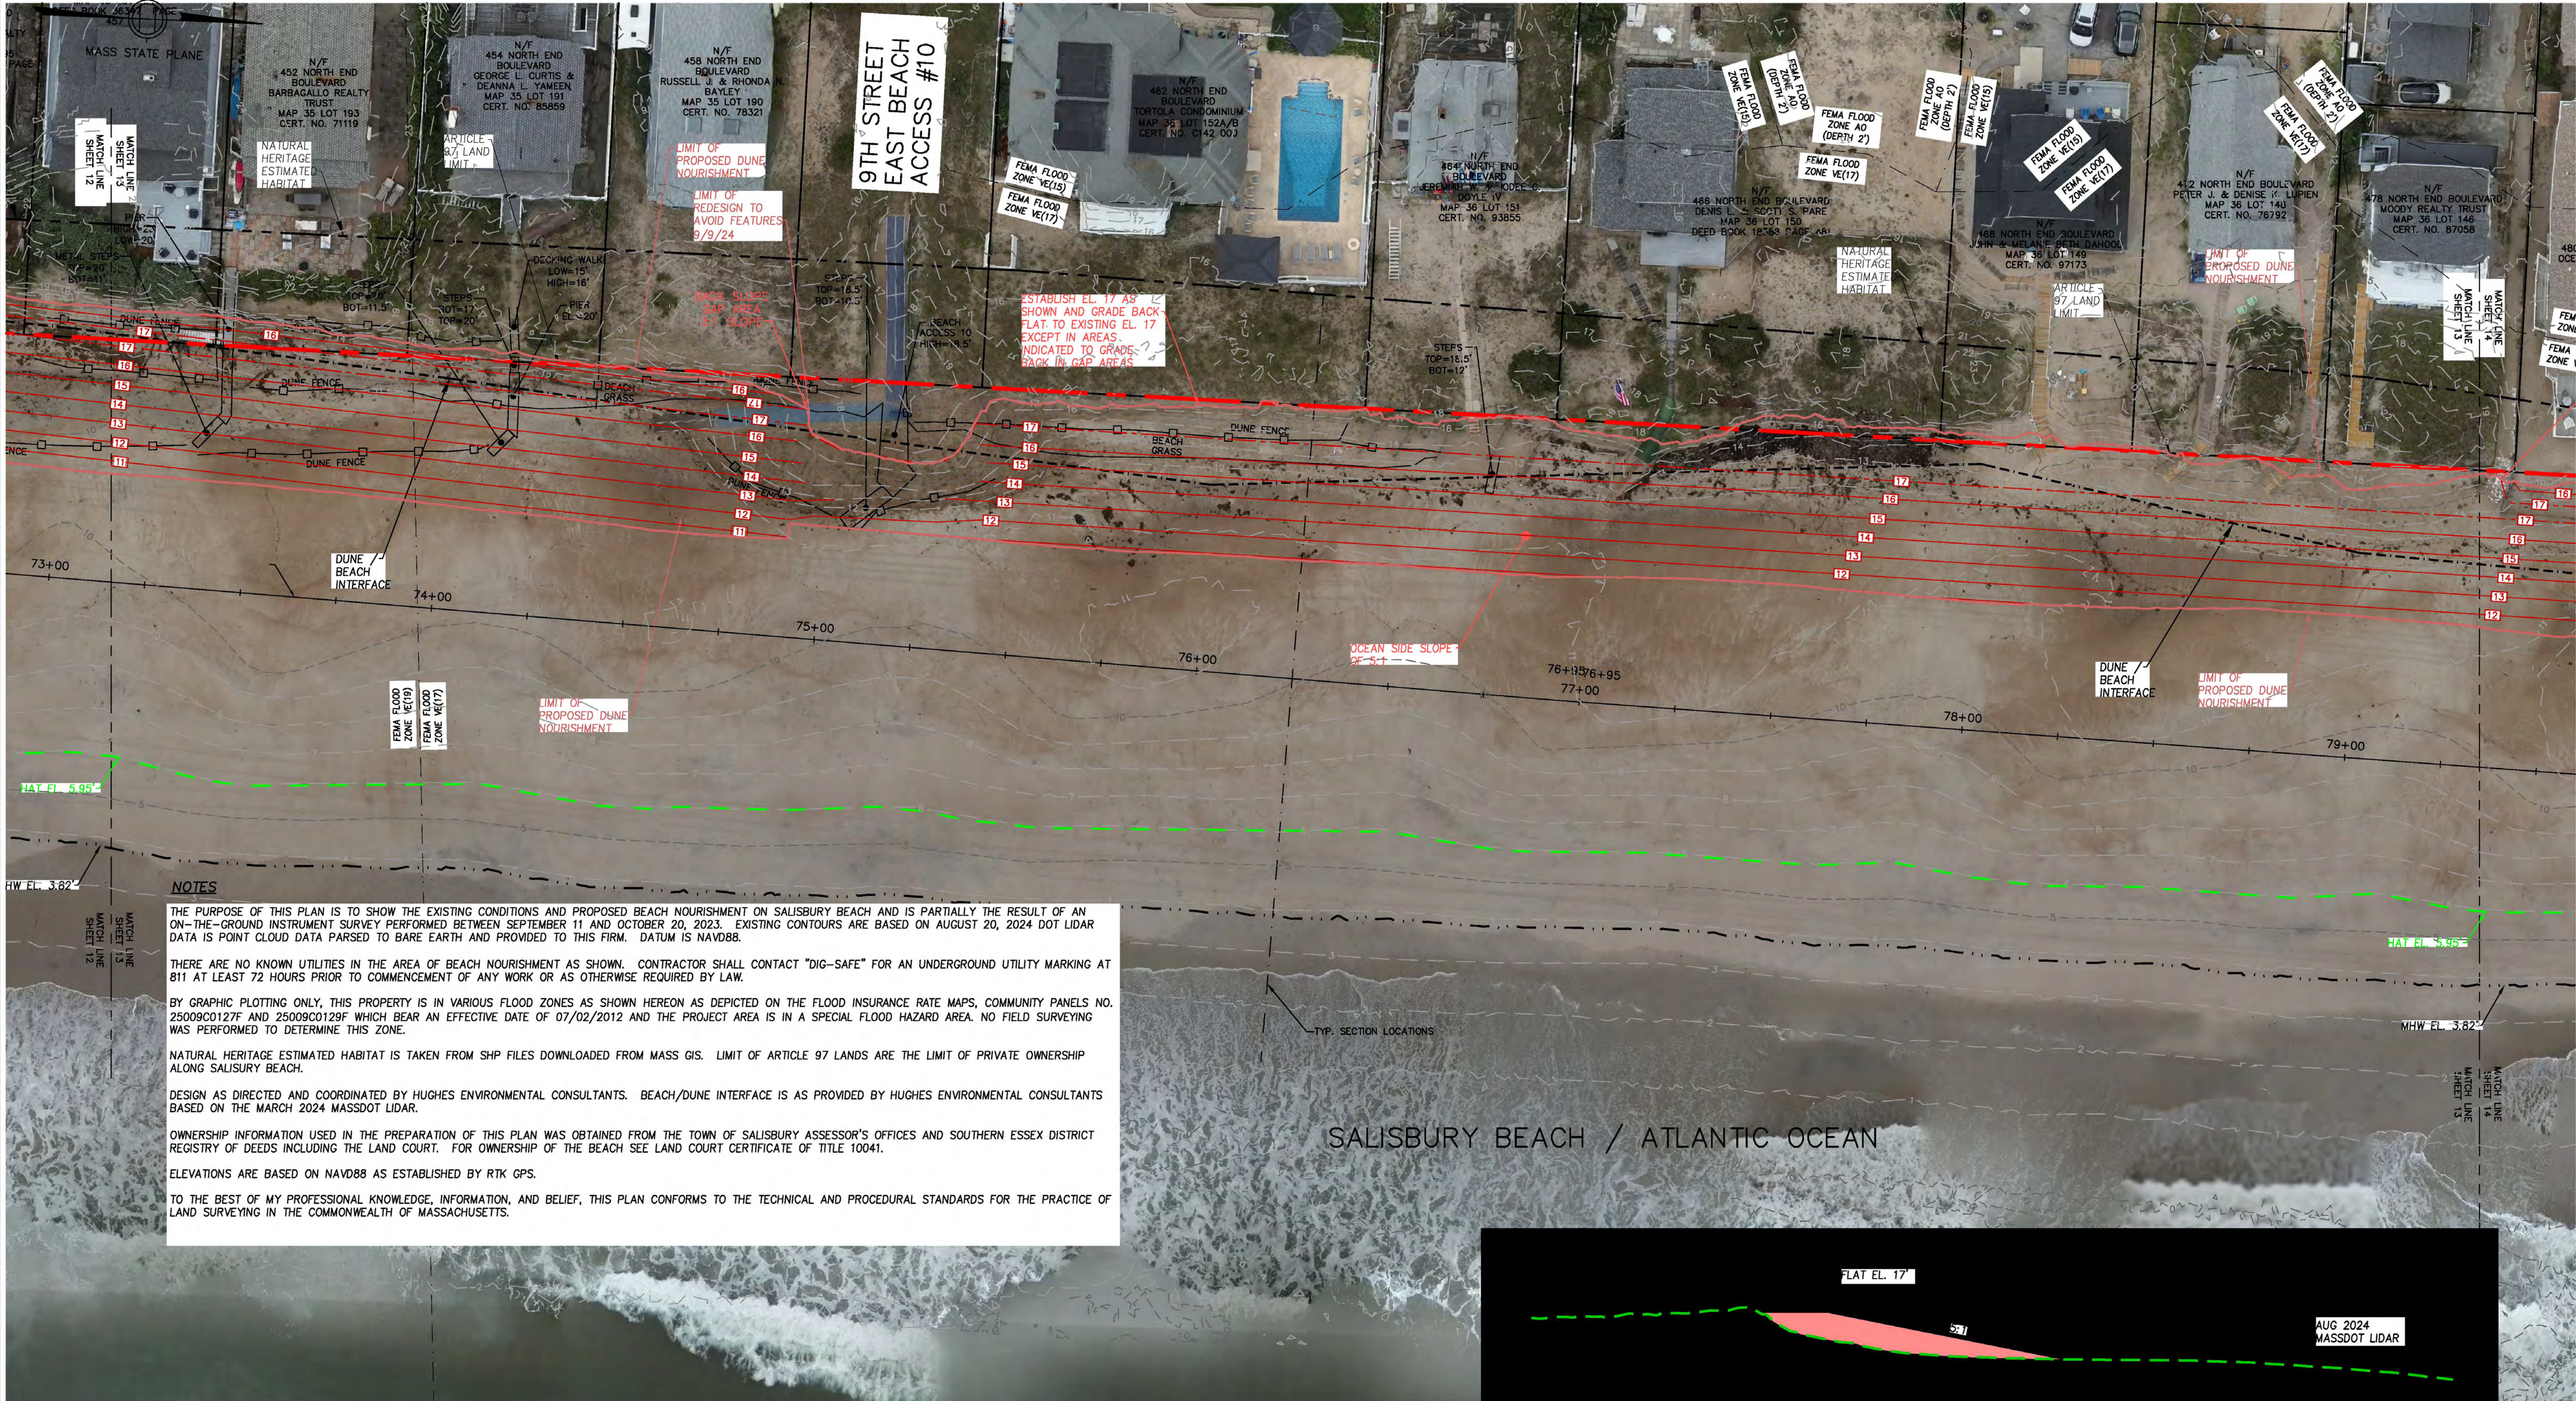

NOTES

THE PURPOSE OF THIS PLAN IS TO SHOW THE EXISTING CONDITIONS AND PROPOSED BEACH NOURISHMENT ON SALISBURY BEACH AND IS PARTIALLY THE RESULT OF AN ON-THE-GROUND INSTRUMENT SURVEY PERFORMED BETWEEN SEPTEMBER 11 AND OCTOBER 20, 2023. EXISTING CONTOURS ARE BASED ON AUGUST 20, 2024 DOT LIDAR DATA IS POINT CLOUD DATA PARSED TO BARE EARTH AND PROVIDED TO THIS FIRM. DATUM IS NAVD88.

THERE ARE NO KNOWN UTILITIES IN THE AREA OF BEACH NOURISHMENT AS SHOWN. CONTRACTOR SHALL CONTACT "DIG-SAFE" FOR AN UNDERGROUND UTILITY MARKING AT 811 AT LEAST 72 HOURS PRIOR TO COMMENCEMENT OF ANY WORK OR AS OTHERWISE REQUIRED BY LAW.

BY GRAPHIC PLOTTING ONLY, THIS PROPERTY IS IN VARIOUS FLOOD ZONES AS SHOWN HEREON AS DEPICTED ON THE FLOOD INSURANCE RATE MAPS, COMMUNITY PANELS NO. 25009C0127F AND 25009C0129F WHICH BEAR AN EFFECTIVE DATE OF 07/02/2012 AND THE PROJECT AREA IS IN A SPECIAL FLOOD HAZARD AREA. NO FIELD SURVEYING WAS PERFORMED TO DETERMINE THIS ZONE.


NATURAL HERITAGE ESTIMATED HABITAT IS TAKEN FROM SHP FILES DOWNLOADED FROM MASS GIS. LIMIT OF ARTICLE 97 LANDS ARE THE LIMIT OF PRIVATE OWNERSHIP ALONG SALISBURY BEACH.

DESIGN AS DIRECTED AND COORDINATED BY HUGHES ENVIRONMENTAL CONSULTANTS. BEACH/DUNE INTERFACE IS AS PROVIDED BY HUGHES ENVIRONMENTAL CONSULTANTS BASED ON THE MARCH 2024 MASSDOT LIDAR.



OWNERSHIP INFORMATION USED IN THE PREPARATION OF THIS PLAN WAS OBTAINED FROM THE TOWN OF SALISBURY ASSESSOR'S OFFICES AND SOUTHERN ESSEX DISTRICT REGISTRY OF DEEDS INCLUDING THE LAND COURT. FOR OWNERSHIP OF THE BEACH SEE LAND COURT CERTIFICATE OF TITLE 10041.

ELEVATIONS ARE BASED ON NAVD88 AS ESTABLISHED BY RTK GPS.

TO THE BEST OF MY PROFESSIONAL KNOWLEDGE, INFORMATION, AND BELIEF, THIS PLAN CONFORMS TO THE TECHNICAL AND PROCEDURAL STANDARDS FOR THE PRACTICE OF LAND SURVEYING IN THE COMMONWEALTH OF MASSACHUSETTS.

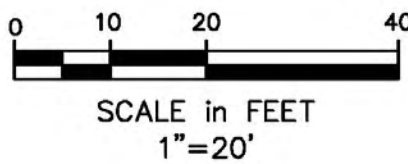

*NOTE THAT ALL PLANIMETRIC DETAIL IS AS GROUND SURVEYED IN OCTOBER 2023 AND MUCH AS BEEN DESTROYED BY SUBSEQUENT STORMS. FIELD ADJUST IN COORDINATION WITH TOWN REPRESENTATIVES AT STRUCTURES IF STILL IN EXISTENCE.

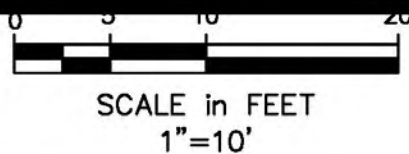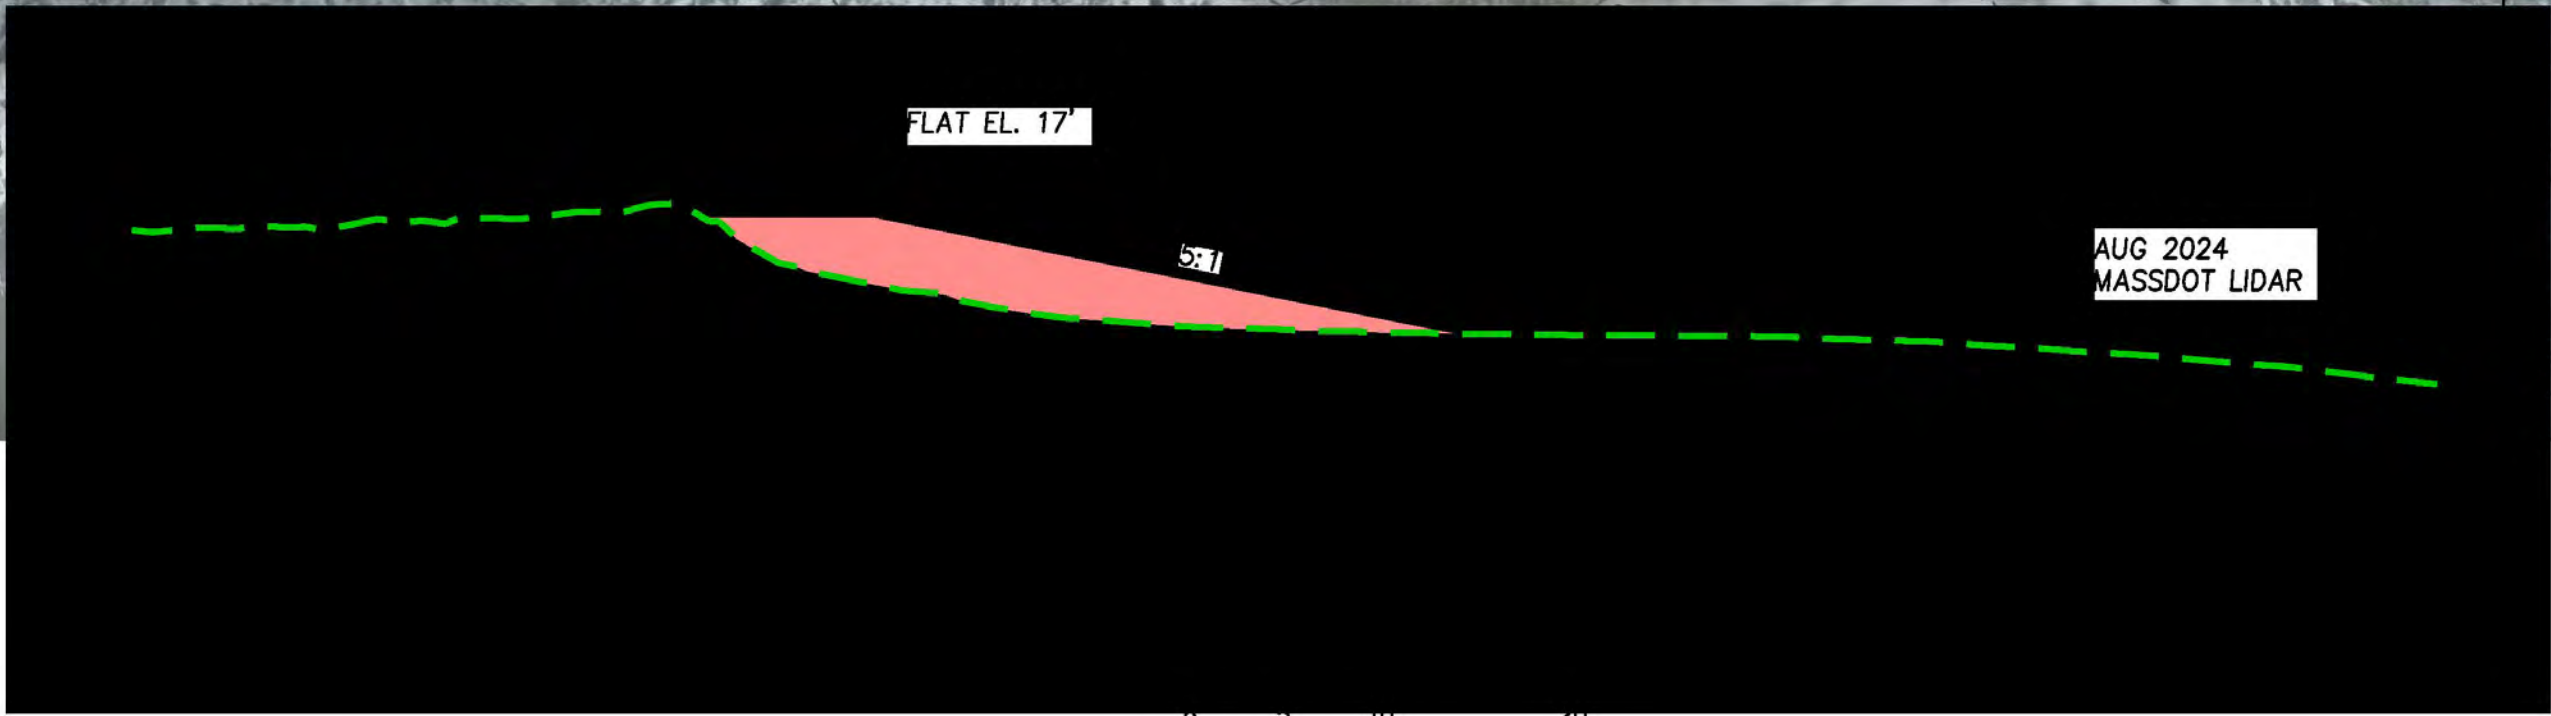

Copyright 2024 Winter GEC, LLC

Winter GEC, LLC

44 MERRIMAC STREET
NEWBURYPORT, MA 01950
978-270-8626

SCALE:
HORIZ: 1"= 20'
VERT: N.A.

NO.	DATE	BY	REVISIONS

FIELD: JK
CALCS: CO/EC
CHECKED: EJC
APPROVED: EJC

CONSERVATION PLAN

SALISBURY BEACH

PLAN OF LAND IN
SALISBURY, MASSACHUSETTS
SURVEYED FOR
HUGHES ENVIRONMENTAL

PROJECT NO.
2023-SAL-BEACH
DATE: AUG 18, 2024
SHEET NO.
13 OF 15



NOTES

THE PURPOSE OF THIS PLAN IS TO SHOW THE EXISTING CONDITIONS AND PROPOSED BEACH NOURISHMENT ON SALISBURY BEACH AND IS PARTIALLY THE RESULT OF AN ON-THE-GROUND INSTRUMENT SURVEY PERFORMED BETWEEN SEPTEMBER 11 AND OCTOBER 20, 2023. EXISTING CONTOURS ARE BASED ON AUGUST 20, 2024 DOT LIDAR DATA IS POINT CLOUD DATA PARSED TO BARE EARTH AND PROVIDED TO THIS FIRM. DATUM IS NAVD88.

THERE ARE NO KNOWN UTILITIES IN THE AREA OF BEACH NOURISHMENT AS SHOWN. CONTRACTOR SHALL CONTACT "DIG-SAFE" FOR AN UNDERGROUND UTILITY MARKING AT 811 AT LEAST 72 HOURS PRIOR TO COMMENCEMENT OF ANY WORK OR AS OTHERWISE REQUIRED BY LAW.

BY GRAPHIC PLOTTING ONLY, THIS PROPERTY IS IN VARIOUS FLOOD ZONES AS SHOWN HEREON AS DEPICTED ON THE FLOOD INSURANCE RATE MAPS, COMMUNITY PANELS NO. 25009C0127F AND 25009C0129F WHICH BEAR AN EFFECTIVE DATE OF 07/02/2012 AND THE PROJECT AREA IS IN A SPECIAL FLOOD HAZARD AREA. NO FIELD SURVEYING WAS PERFORMED TO DETERMINE THIS ZONE.

NATURAL HERITAGE ESTIMATED HABITAT IS TAKEN FROM SHP FILES DOWNLOADED FROM MASS GIS. LIMIT OF ARTICLE 97 LANDS ARE THE LIMIT OF PRIVATE OWNERSHIP ALONG SALISBURY BEACH.



DESIGN AS DIRECTED AND COORDINATED BY HUGHES ENVIRONMENTAL CONSULTANTS. BEACH/DUNE INTERFACE IS AS PROVIDED BY HUGHES ENVIRONMENTAL CONSULTANTS BASED ON THE MARCH 2024 MASSDOT LIDAR.

OWNERSHIP INFORMATION USED IN THE PREPARATION OF THIS PLAN WAS OBTAINED FROM THE TOWN OF SALISBURY ASSESSOR'S OFFICES AND SOUTHERN ESSEX DISTRICT REGISTRY OF DEEDS INCLUDING THE LAND COURT. FOR OWNERSHIP OF THE BEACH SEE LAND COURT CERTIFICATE OF TITLE 10041.

ELEVATIONS ARE BASED ON NAVD88 AS ESTABLISHED BY RTK GPS.

TO THE BEST OF MY PROFESSIONAL KNOWLEDGE, INFORMATION, AND BELIEF, THIS PLAN CONFORMS TO THE TECHNICAL AND PROCEDURAL STANDARDS FOR THE PRACTICE OF LAND SURVEYING IN THE COMMONWEALTH OF MASSACHUSETTS.

SALISBURY BEACH / ATLANTIC OCEAN

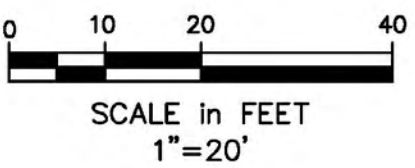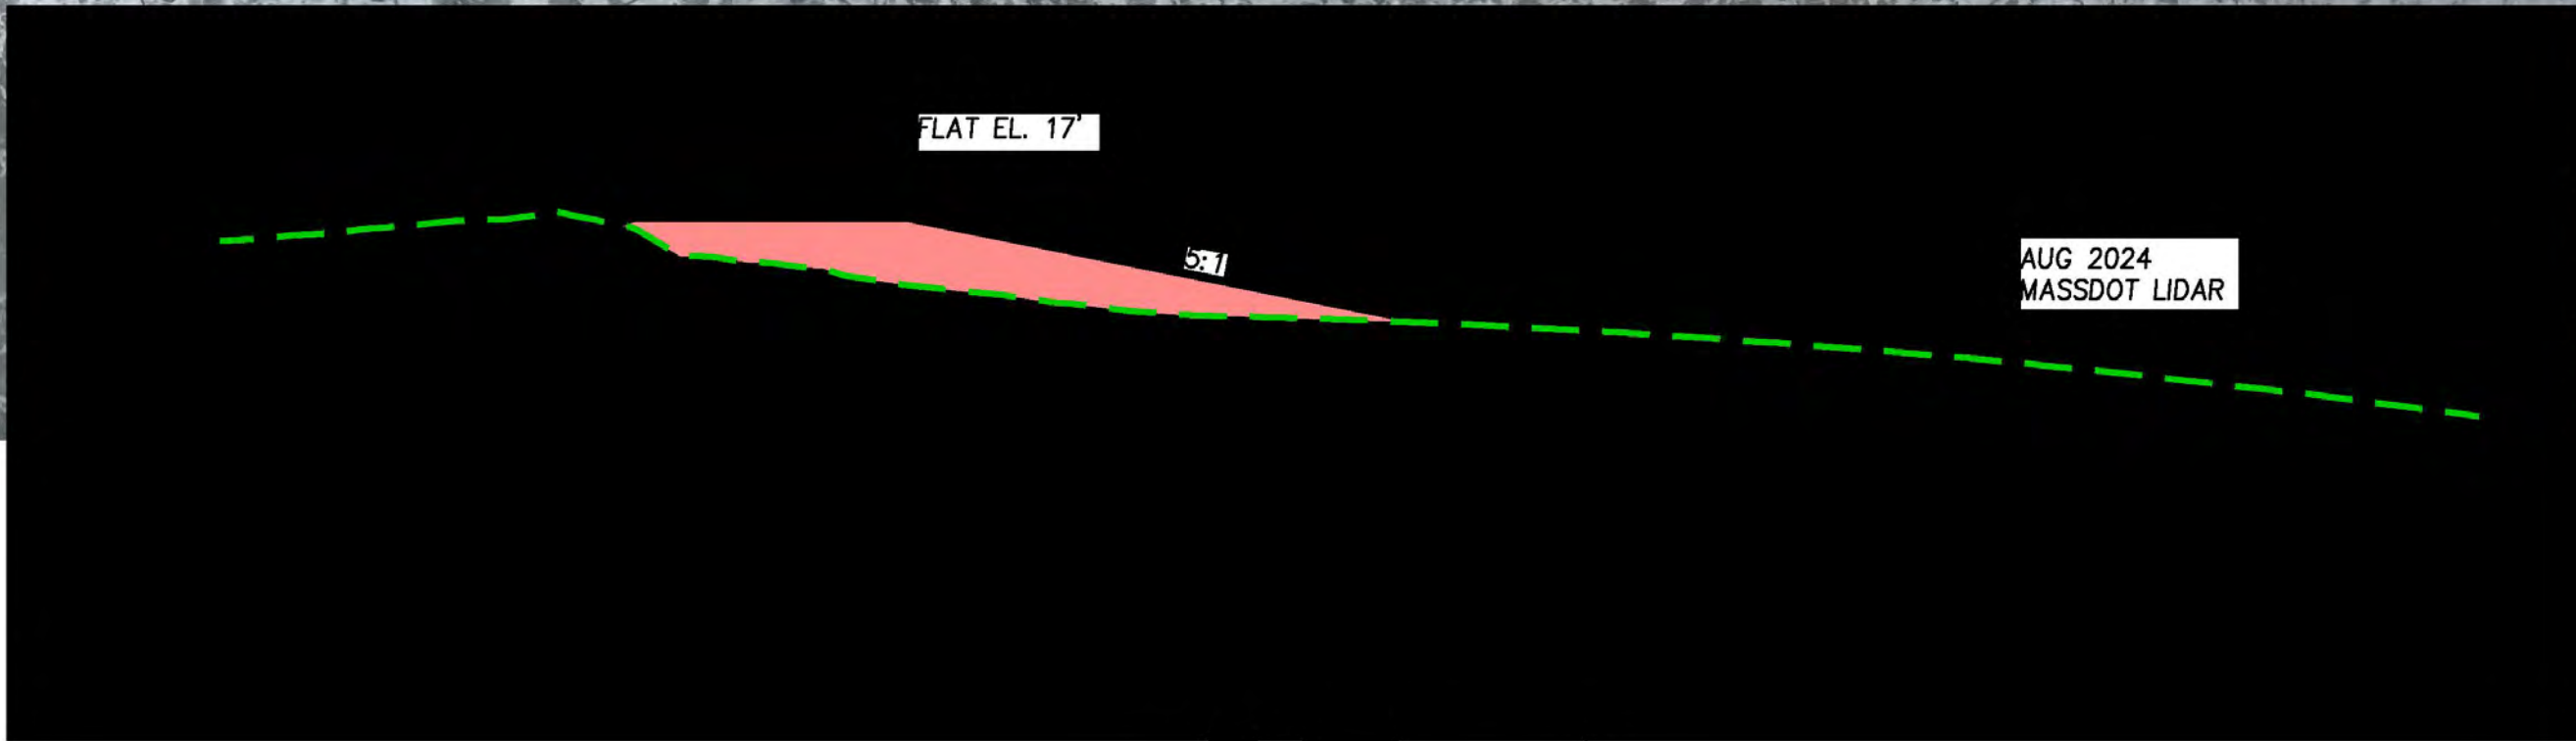

*NOTE THAT ALL PLANIMETRIC DETAIL IS AS GROUND SURVEYED IN OCTOBER 2023 AND MUCH AS BEEN DESTROYED BY SUBSEQUENT STORMS. FIELD ADJUST IN COORDINATION WITH TOWN REPRESENTATIVES AT STRUCTURES IF STILL IN EXISTENCE.

SCALE in FEET
1"=10'

Copyright 2024 Winter GEC, LLC

Winter GEC, LLC

44 MERRIMAC STREET
NEWBURYPORT, MA 01950
978-270-8626

SCALE:
HORIZ: 1"= 20'
VERT: N.A.

NO.	DATE	BY	REVISIONS

FIELD: JK
CALCS: CO/EC
CHECKED: EJC
APPROVED: EJC

CONSERVATION PLAN

SALISBURY BEACH

PLAN OF LAND IN
SALISBURY, MASSACHUSETTS
SURVEYED FOR
HUGHES ENVIRONMENTAL

PROJECT NO.
2023-SAL-BEACH
DATE: AUG 18, 2024
SHEET NO.
14 OF 15

